


מס', מהות העדכון	תאריך	
1		
2		

רשימת תפוצה		מס'	תפקיד	שם	מס' תאריך	1	2	3	4	5	6
1	מזמין										
2	אדריכלות			אלכס ויסמן גדי ענבי							
3	קונסט'										
4	אינסט'										
5	חשמל										
6	מודד										
7	קרקע										
8	קבלן										
	פיקוח - אתר -										

© כל זכויות שמורות למשרד ענבי ויסמן אדריכלים
הקבלן אחראי למידות, ועליו לבקר אותן ולהודיע למתכנן על כל
שעות, ססיה, סתירה או אי-התאמה בסרט ימשיך בעבודתו.
השימוש בתכנית זו רק בהסכמתו המפורשת של המתכנן.
אין לקבוע גדלים ע"י מדידה בשרטוט.

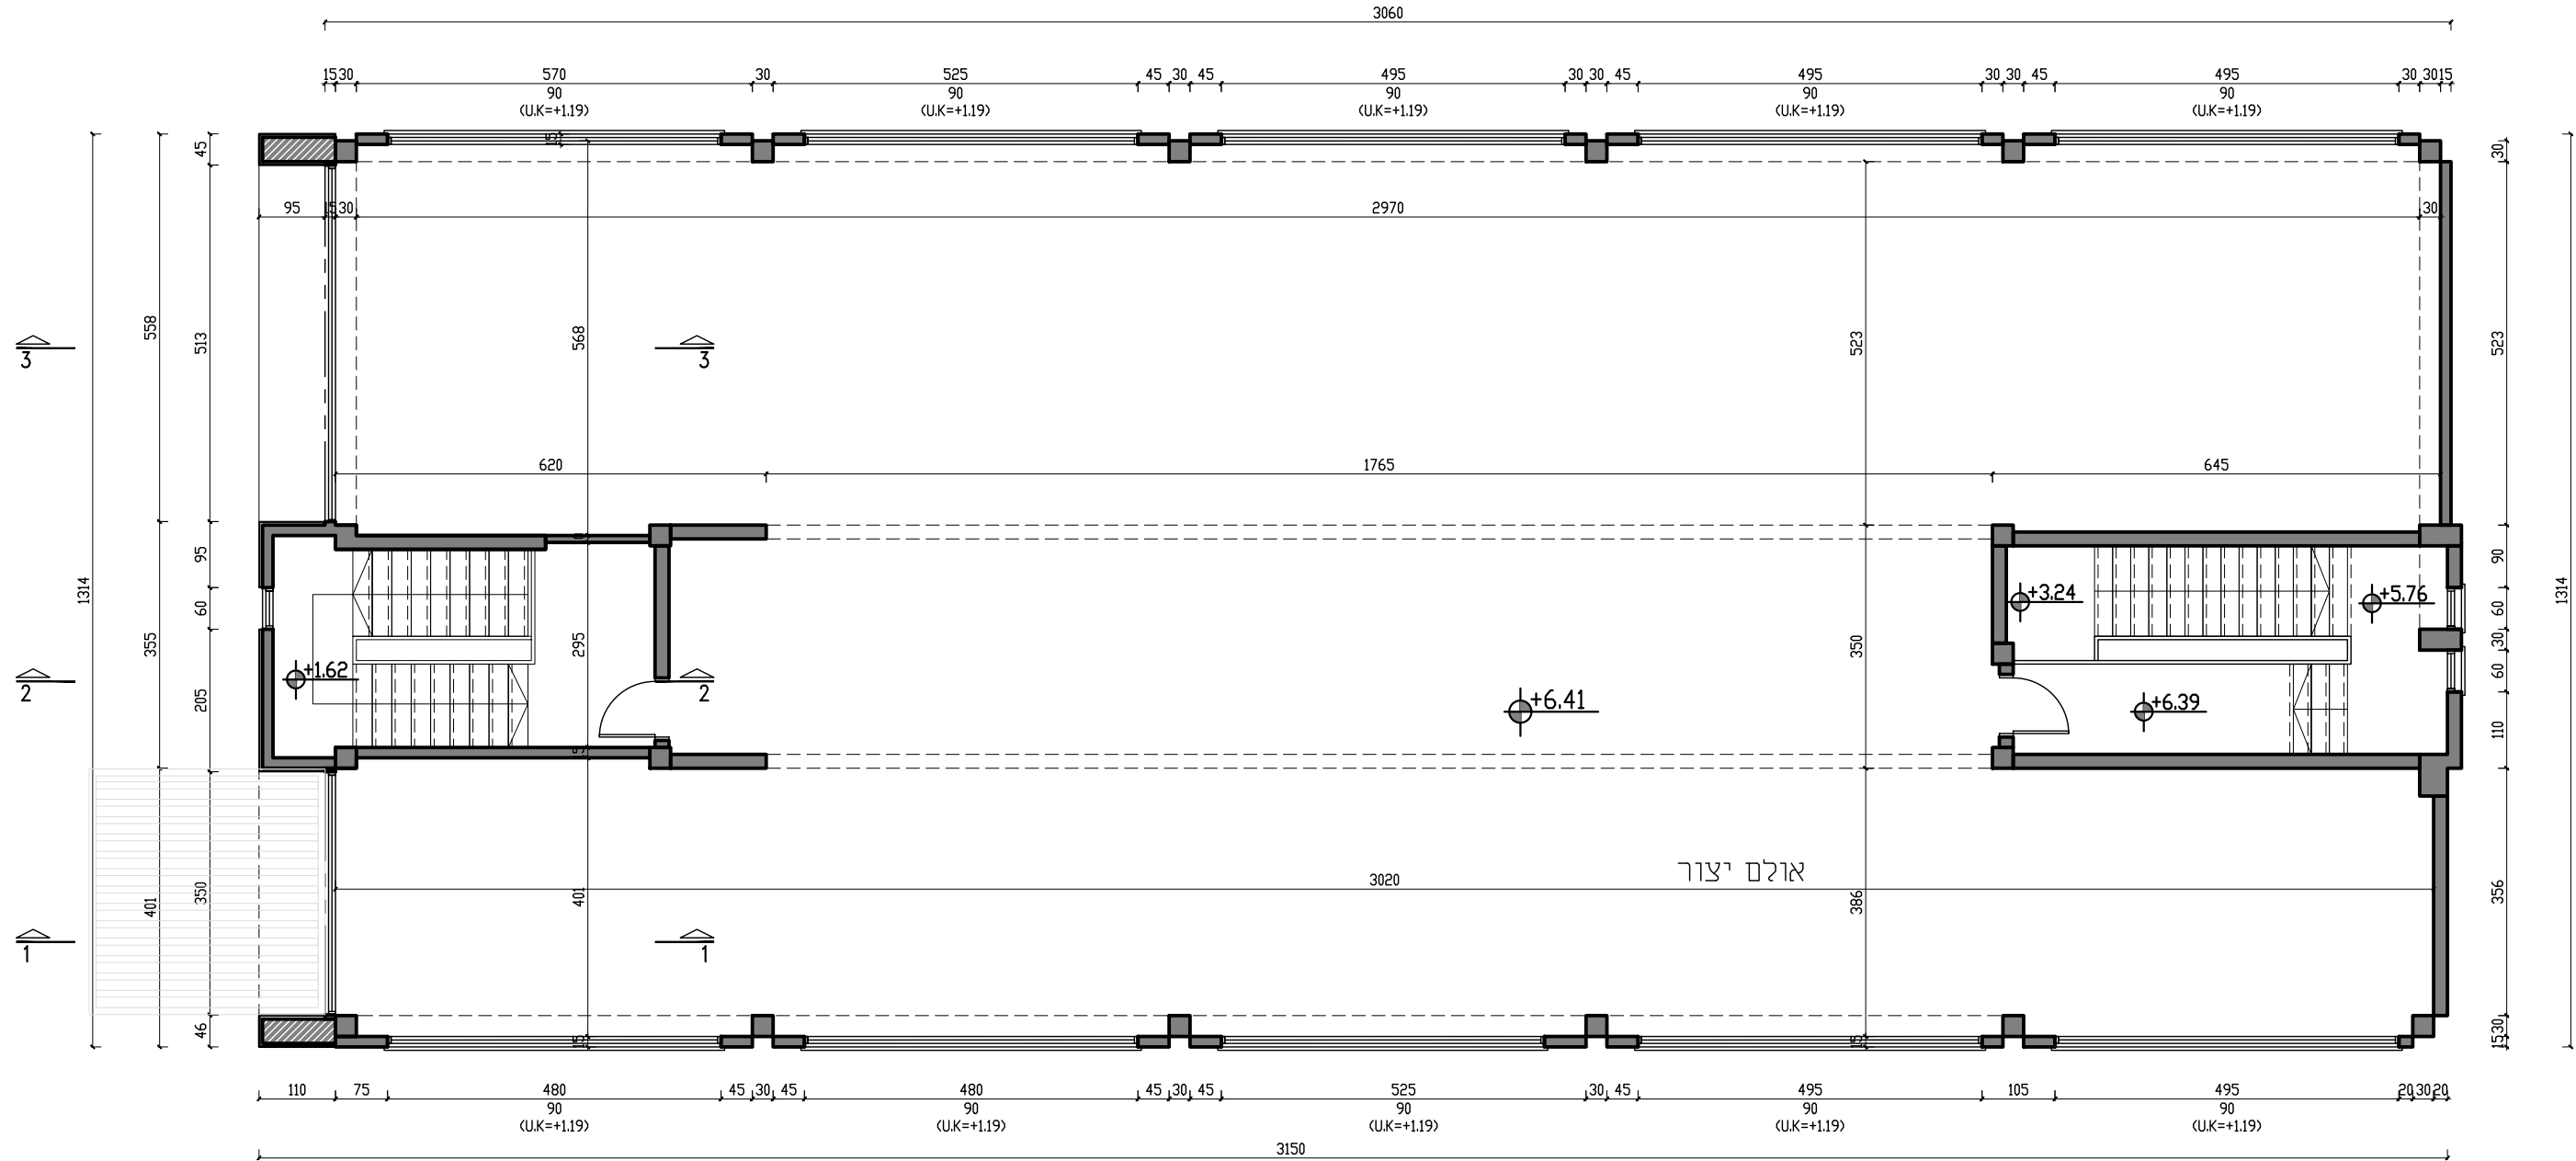

תכנית קומה ב'

קנ"מ 1:100

מהדורה	2	1	4		
	2	1	0	P	L

שם התכנית:

תכניות

תכנית קומה ב' + גגות

קנ"מ:

1:100

לביצוע
למכר
לאישור


תוכנן ע"י: אלכס ויסמן	בוקר ע"י: אלכס ויסמן
אדריכל אחראי במשרד: אלכס ויסמן	אושר ע"י: אלכס ויסמן
תאריך: 25.01.18	תאריך עדכון: 19.09.2022
שם וטופס: 412-TRUFA-NETANYA.dwg	מידות גליון:
קבצים יש לשלוח לכתובת: alex@weismanarch.com	

תרוכה , 4

נתניה



ויסמן אדריכלים
מוריה 46, חיפה
052-3302396 אלכס

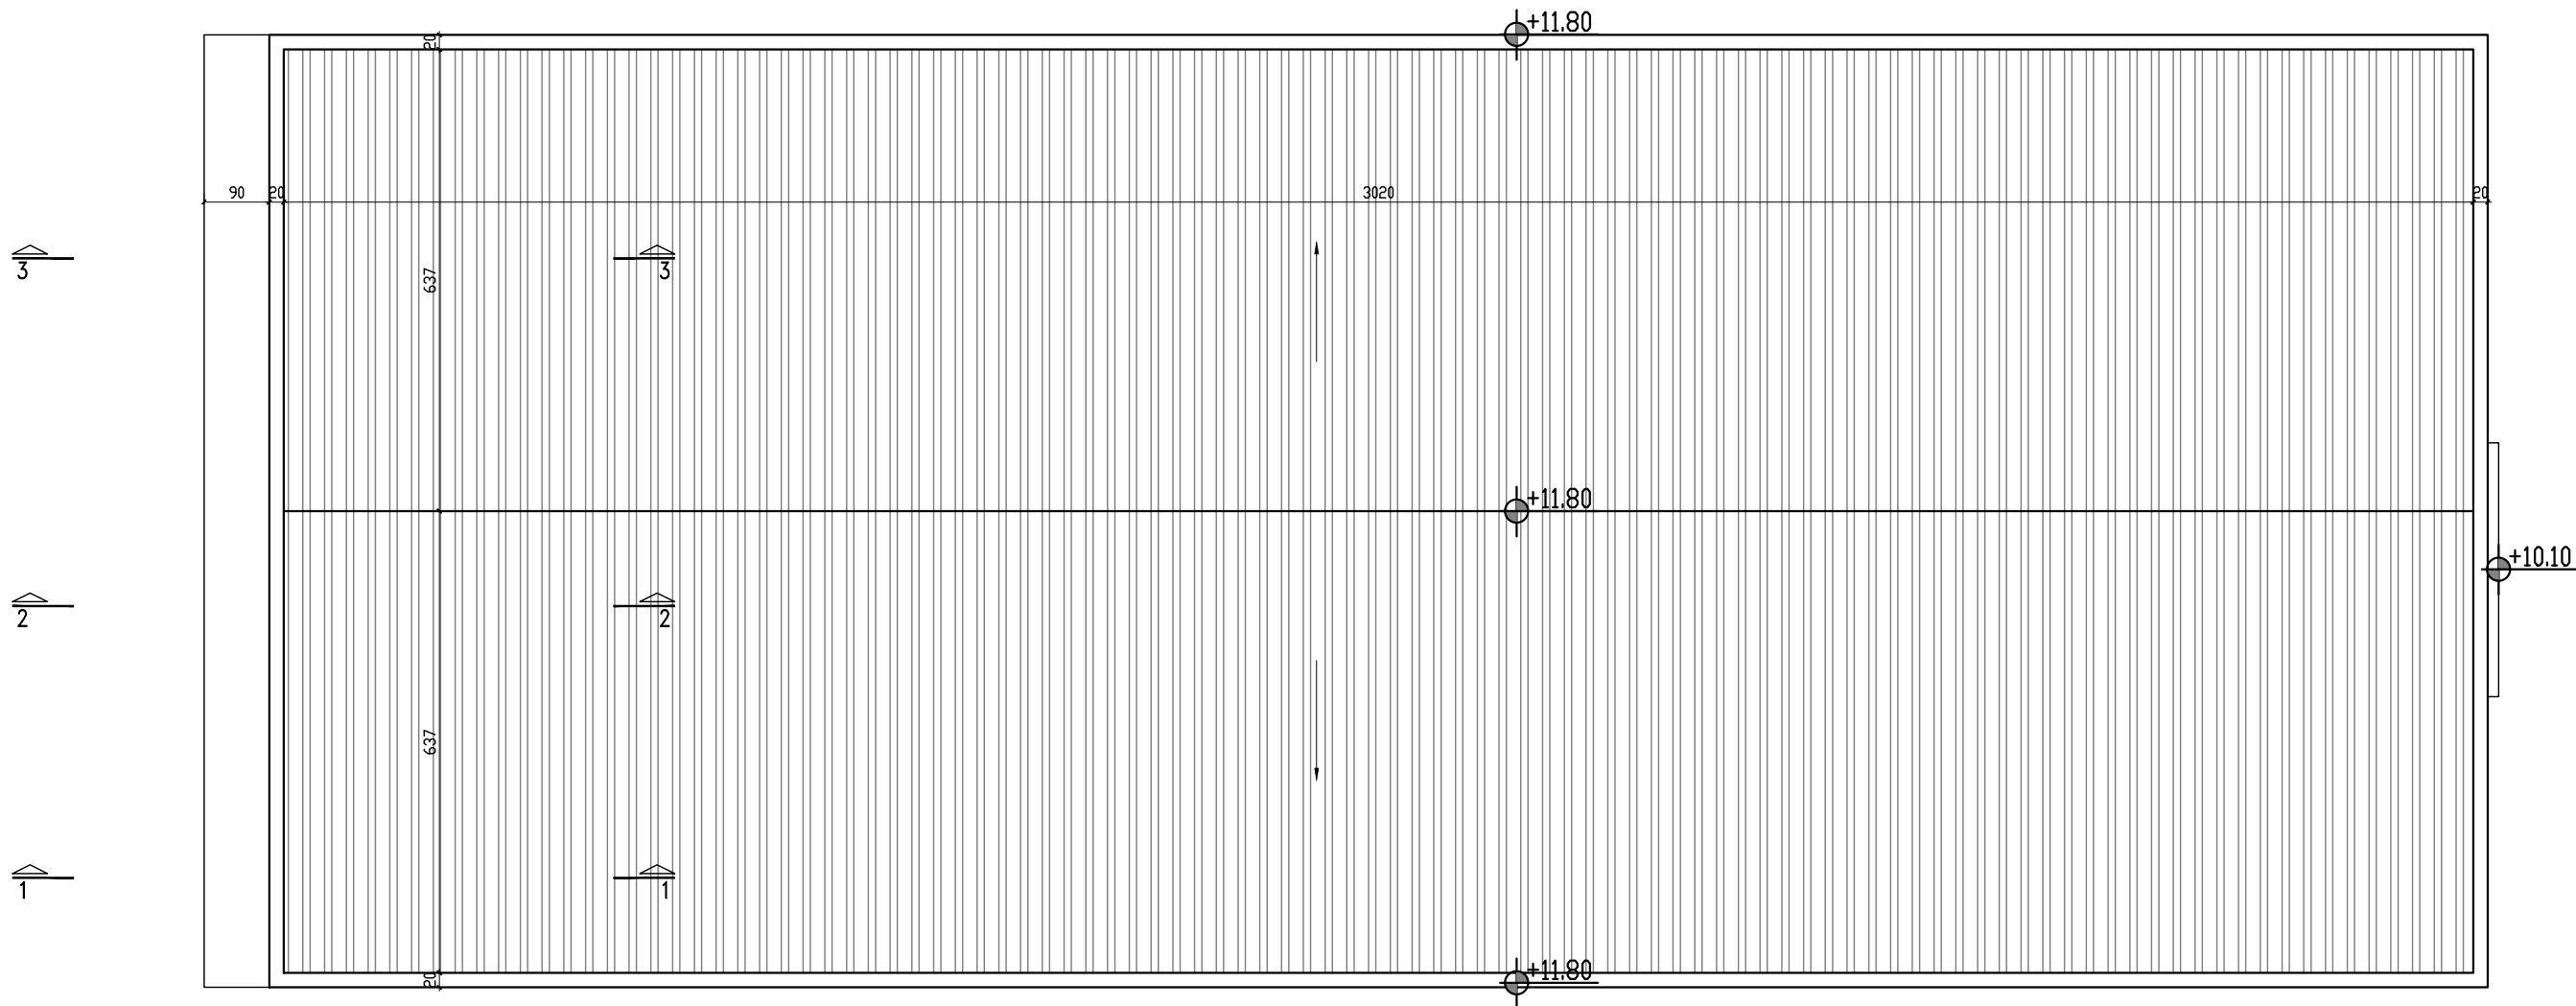

תכנית גגות

קנ"מ 1:100