



מס	מרות העדכון	תאריך
1		
2		

רשימת תפוצה		מס	1	2	3	4	5	6
מס	תפקיד	שם	אריך					
1	מזמין							
2	אדריכלות	אלכס ויסמן						
3	קונסט'							
4	אינסט'							
5	חשמכ							
6	מודד							
7	קדשע							
8	מכני							
	פיקוח -							
	אתר -							


כל זכויות שמורות למשרד ענבי ויסמן אדריכלים
הגבין אחראי למידות, ועליו לבקר 'אתר' ולהודיע למתכנן על כל
שעות, סטיה, סתירה או אי-התאמה בסרט יתשרך בעבודתו.
העומש בתכנית זו רק בהסמכתו המפורשת של המתכנן.
אין לקבוע גדלים ע"י מדידה בשטח.

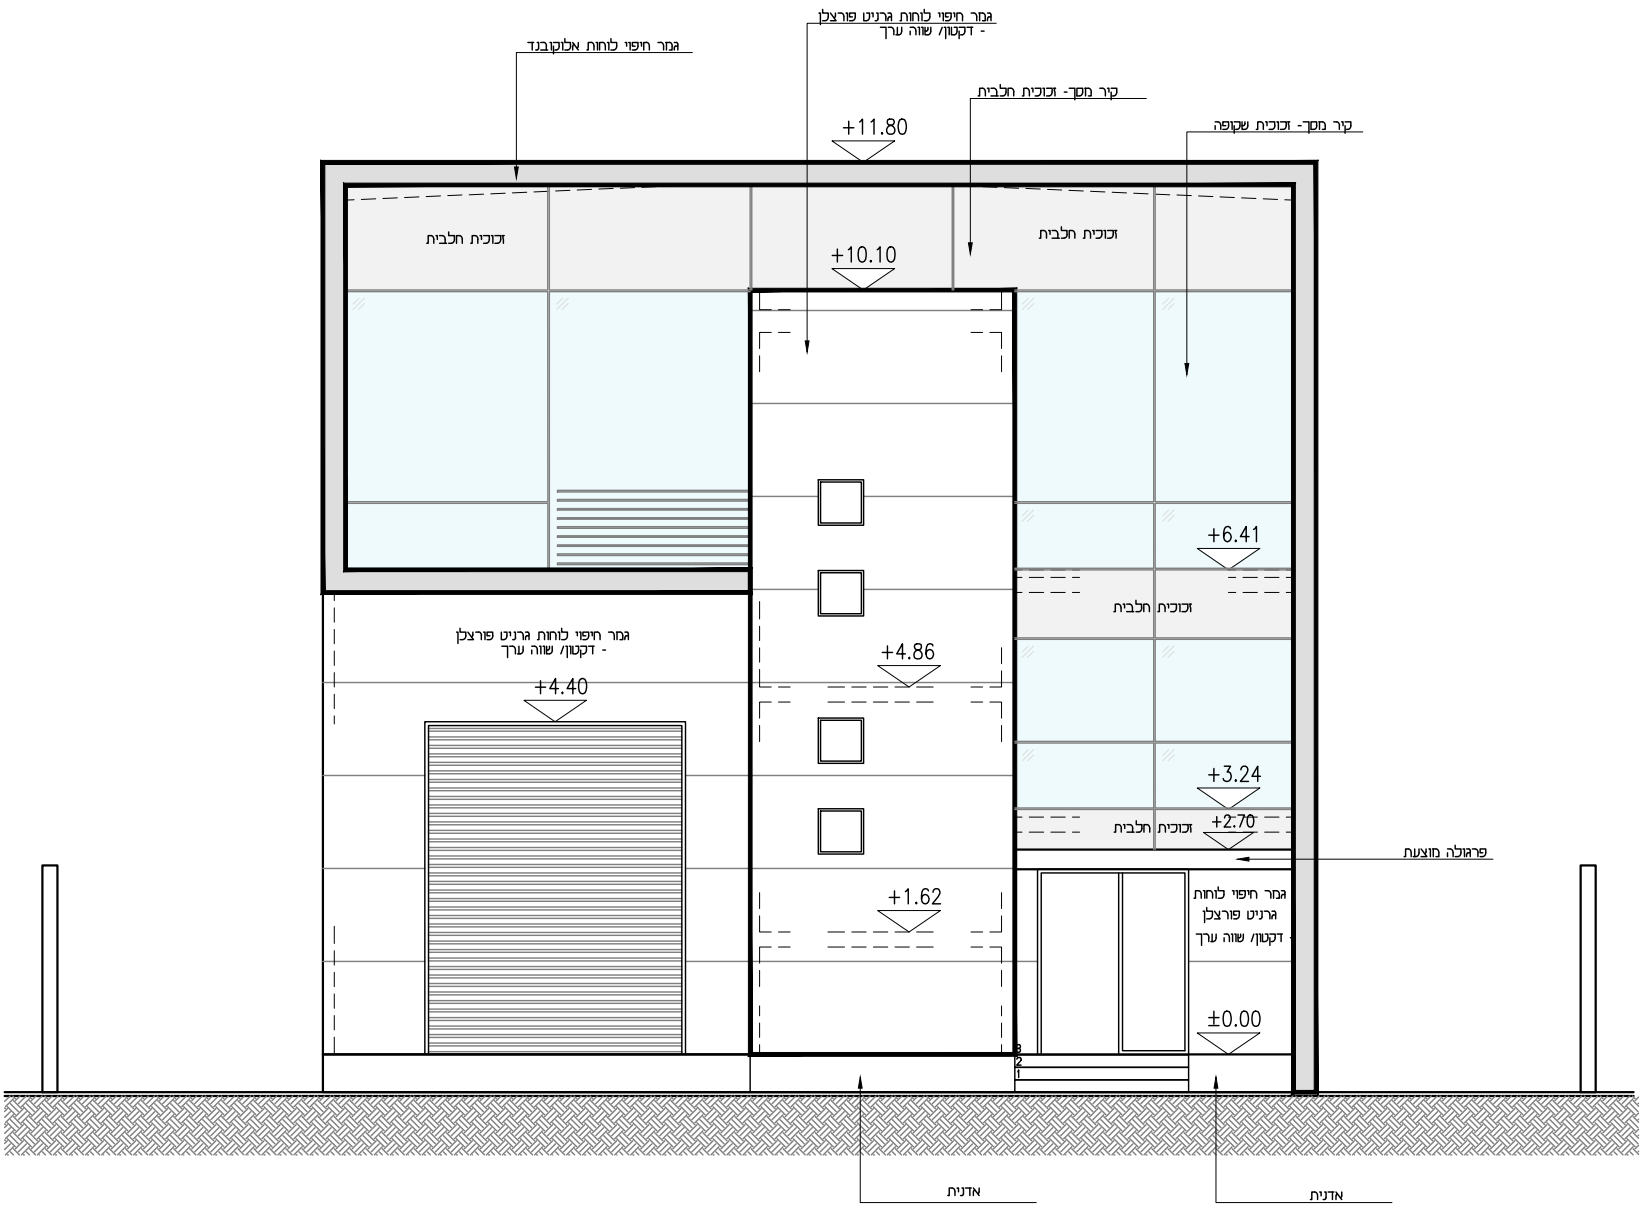


חזית דרומית
קנ"מ 1:100

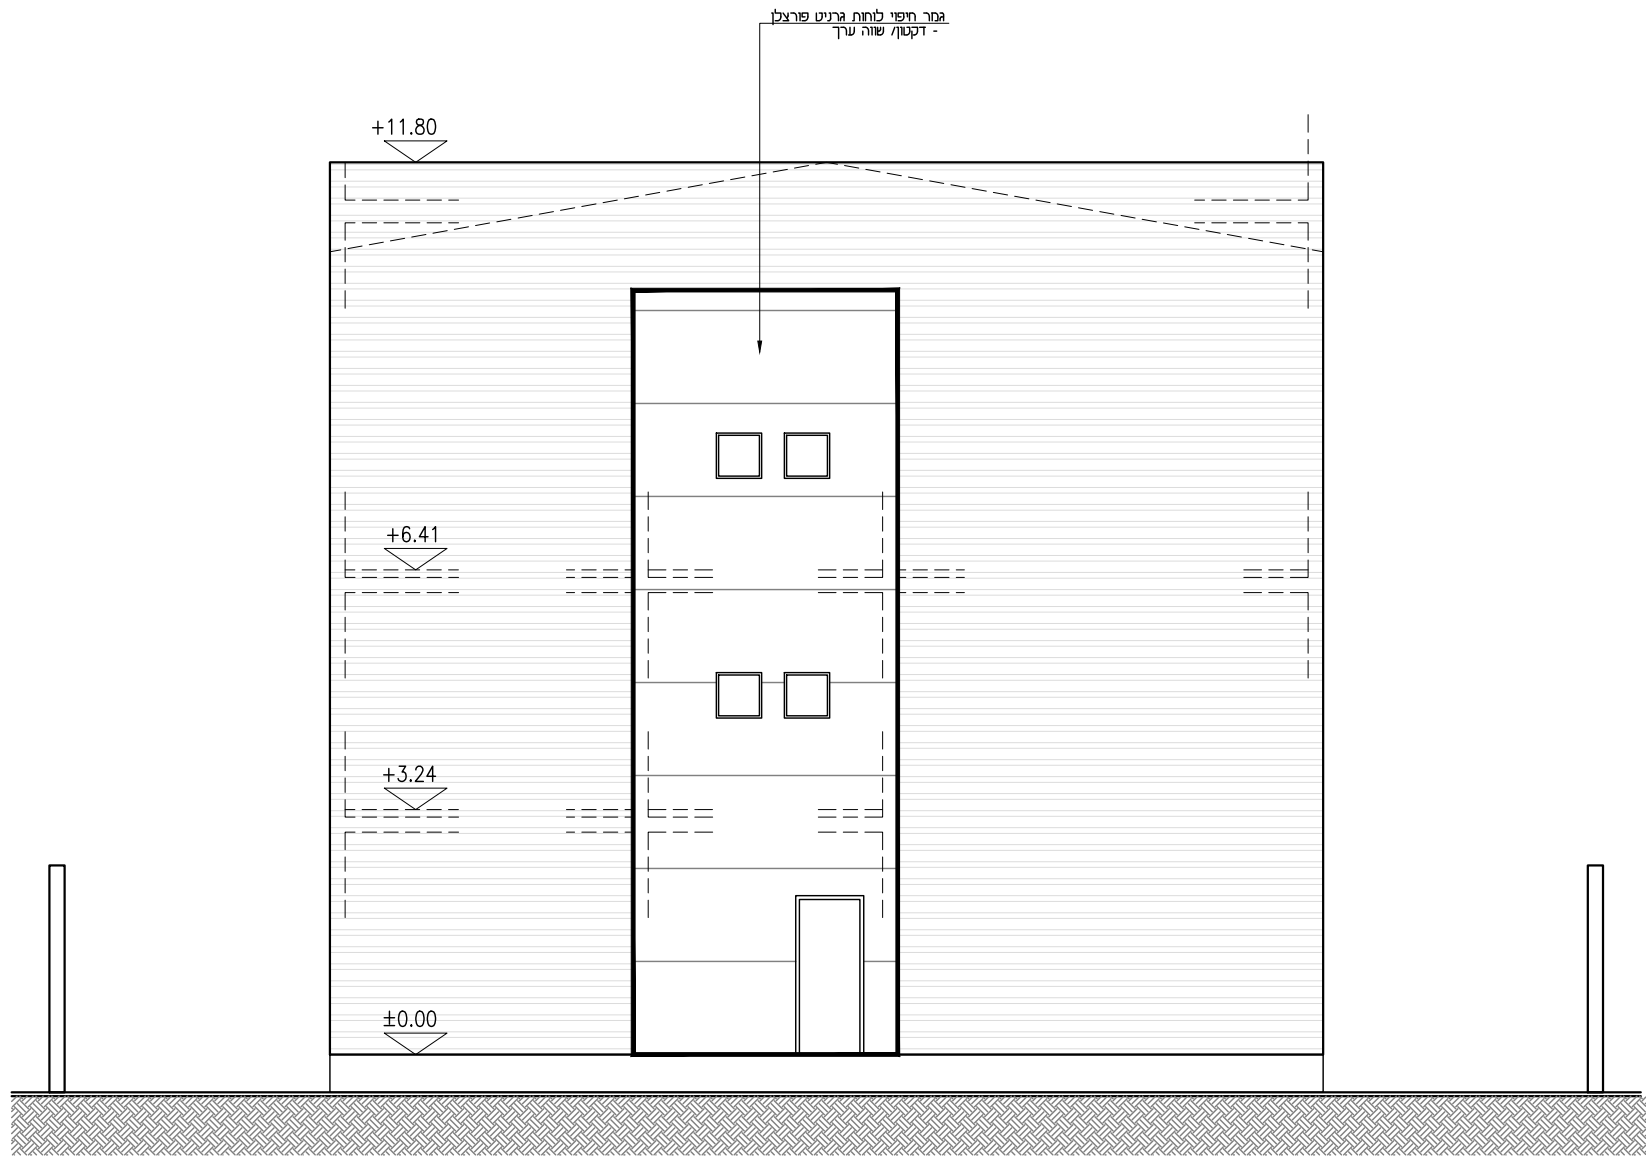

חזית צפונית
קנ"מ 1:100

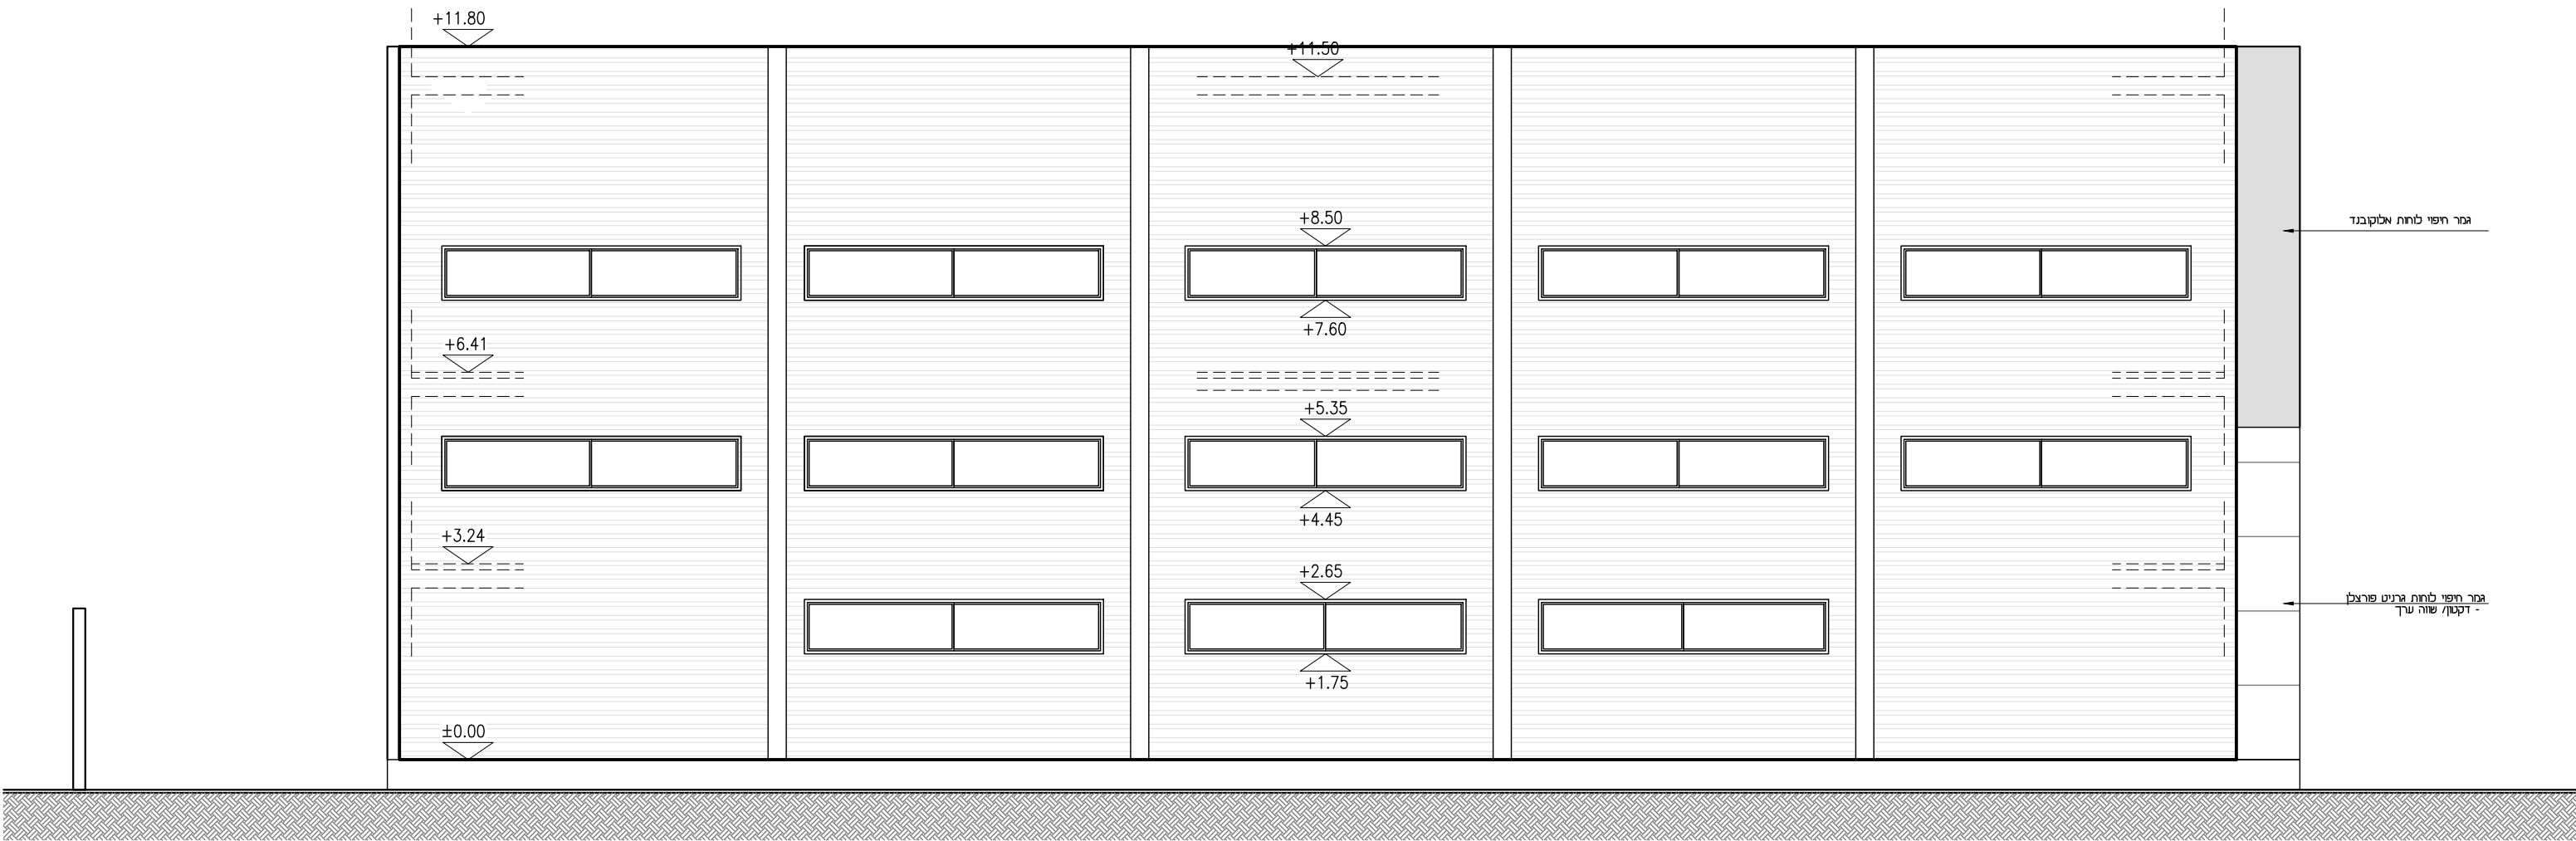

חזית מזרחית
קנ"מ 1:100

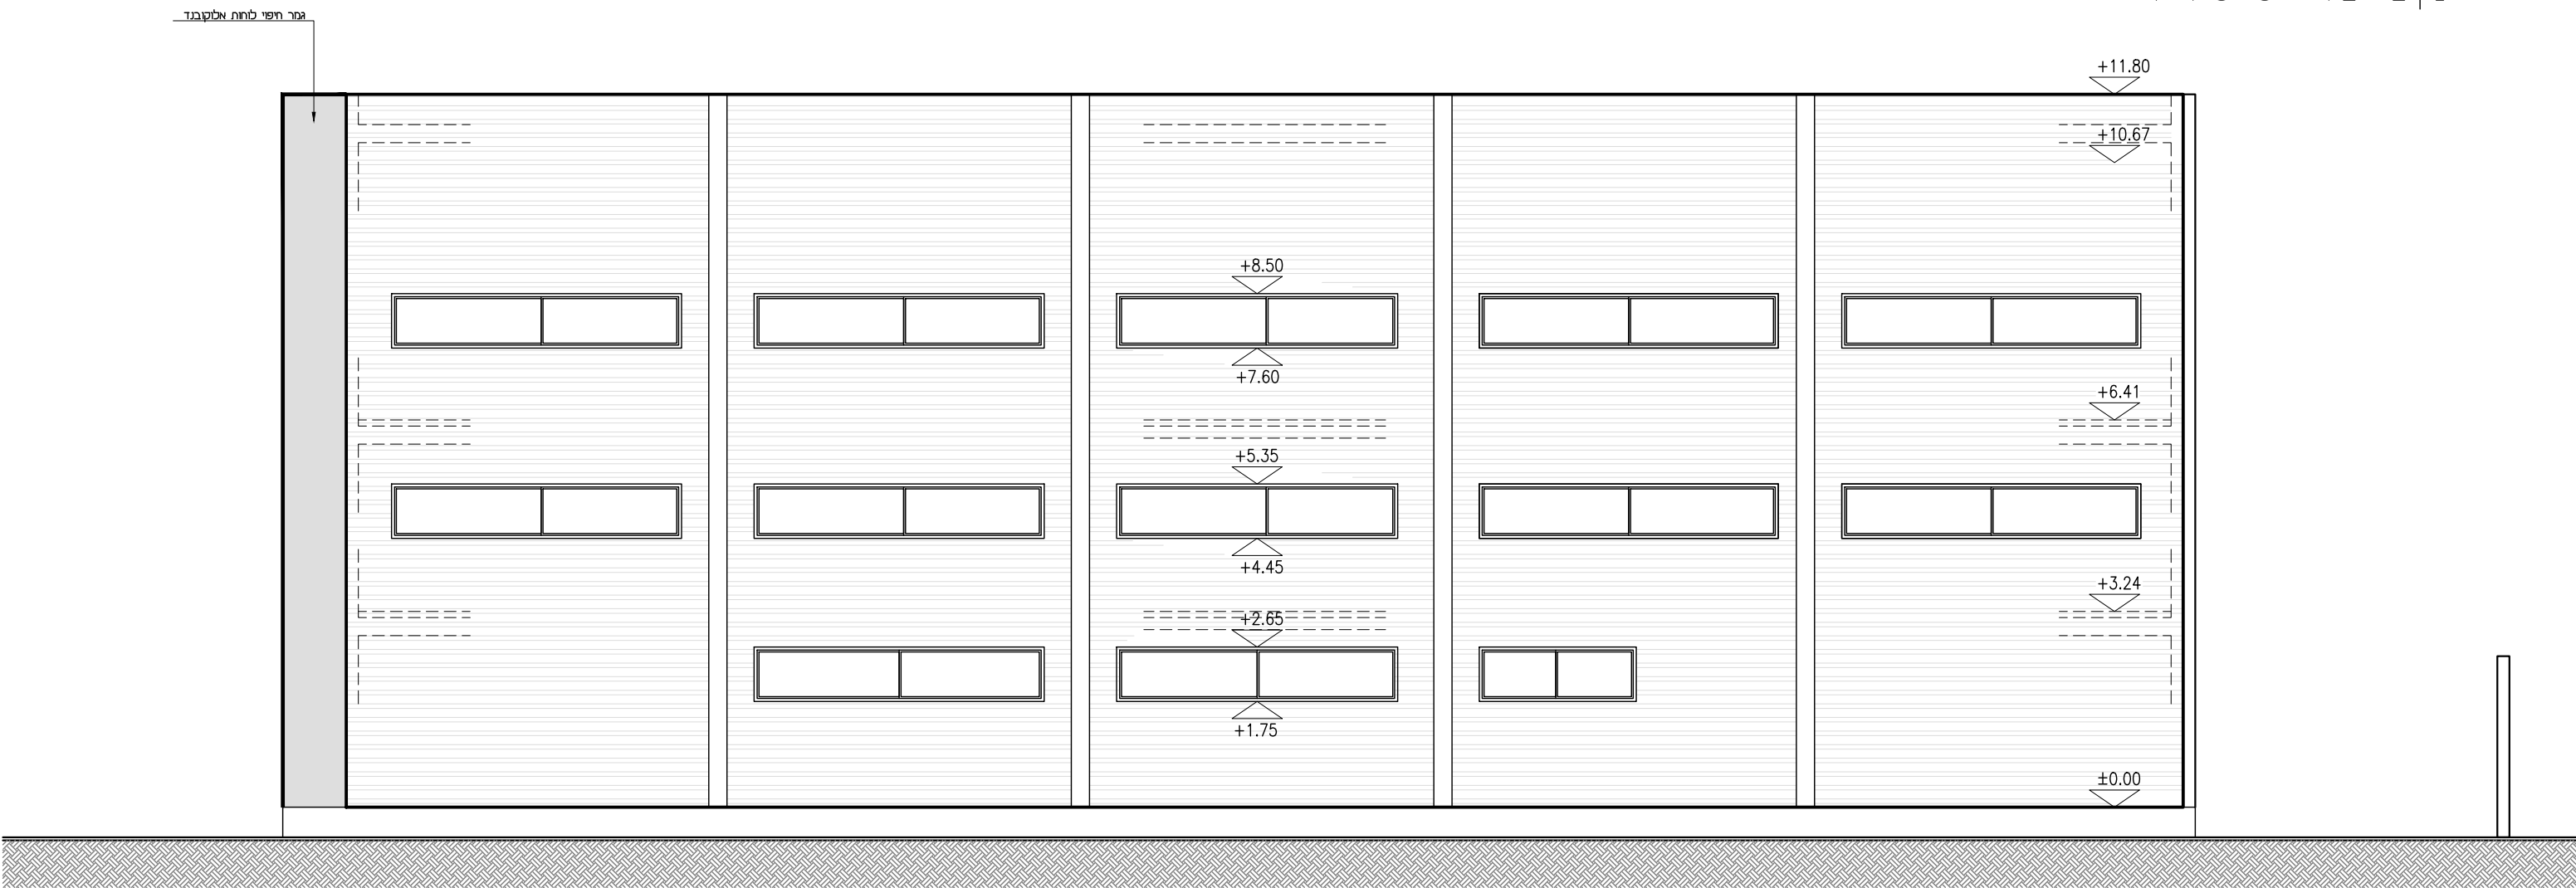

חזית מערבית
קנ"מ 1:100

מחזור	2	1	4	
PL	1	0	3	
שם החברה:				
חזיתות				
קנ"מ	1:100	למשך	לביצוע	
תוכן ע"י: אלכס ויסמן		בוקר ע"י: אלכס ויסמן		
אדריכל אחראי במשרד: אלכס ויסמן		אשר ע"י: אלכס ויסמן		
תאריך: 19.09.2022		תאריך עדכון: 19.09.2022		
מסמך: 412-TRUFA-NETANYA		מדידת גליון: alex@weismanarch.com		
קבצים יש לשלוח לכתובת: alex@weismanarch.com				
תרופה, 4 נתניה				
ויסמן אדריכלים מורה 46, חסה 052-3302396				