

מס, מרות העדכון	תאריך
1	
2	

רשימת תפוצה		מס	1	2	3	4	5	6
מס	תפקיד	שם	תאריך					
			1	2	3	4	5	6
1	מזמין							
2	אדריכלות	אלכס ויסמן גדי ענבי						
3	קונסט'							
4	אינסט'							
5	חשמל							
6	מודד							
7	קרקע							
8	קבלן							
	פיקוח -							
	- אתר							

© כל זכויות שמורות למשרד ענבי ויסמן אדריכלים
הקבלן אחראי למידות, ועליו לבקר אותן ולהודיע למתכנן על כל
שנות, סתירה, אי-התאמה בסרט ימשיך בעבודתו.
השימוש בתוכנית זו רק בהסכמתו המפורשת של המתכנן.
אין לקבוע גדלים ע"י מדידה בשרטוט.

מס	1	2	4
PL 101			

שם התכנית:

תכניות

תכנית קומת קרקע+ קומה א'

קני"מ:

1:100

לשיפור

למכרז

לביצוע


תוכנן ע"י: אלכס ויסמן	בוקר ע"י: אלכס ויסמן
אדריכל אחראי במשרד: אלכס ויסמן	אושר ע"י: אלכס ויסמן
תאריך:	25.01.18
שם הקובץ:	412-TRUFA-NETANYA.dwg
קובצים יש לשלוחו לתוכנית: alex@weismanarch.com	

תרופה , 4

נתניה




וייסמן אדריכלים
מוריה 46, חיפה
052-3302396 אלכס

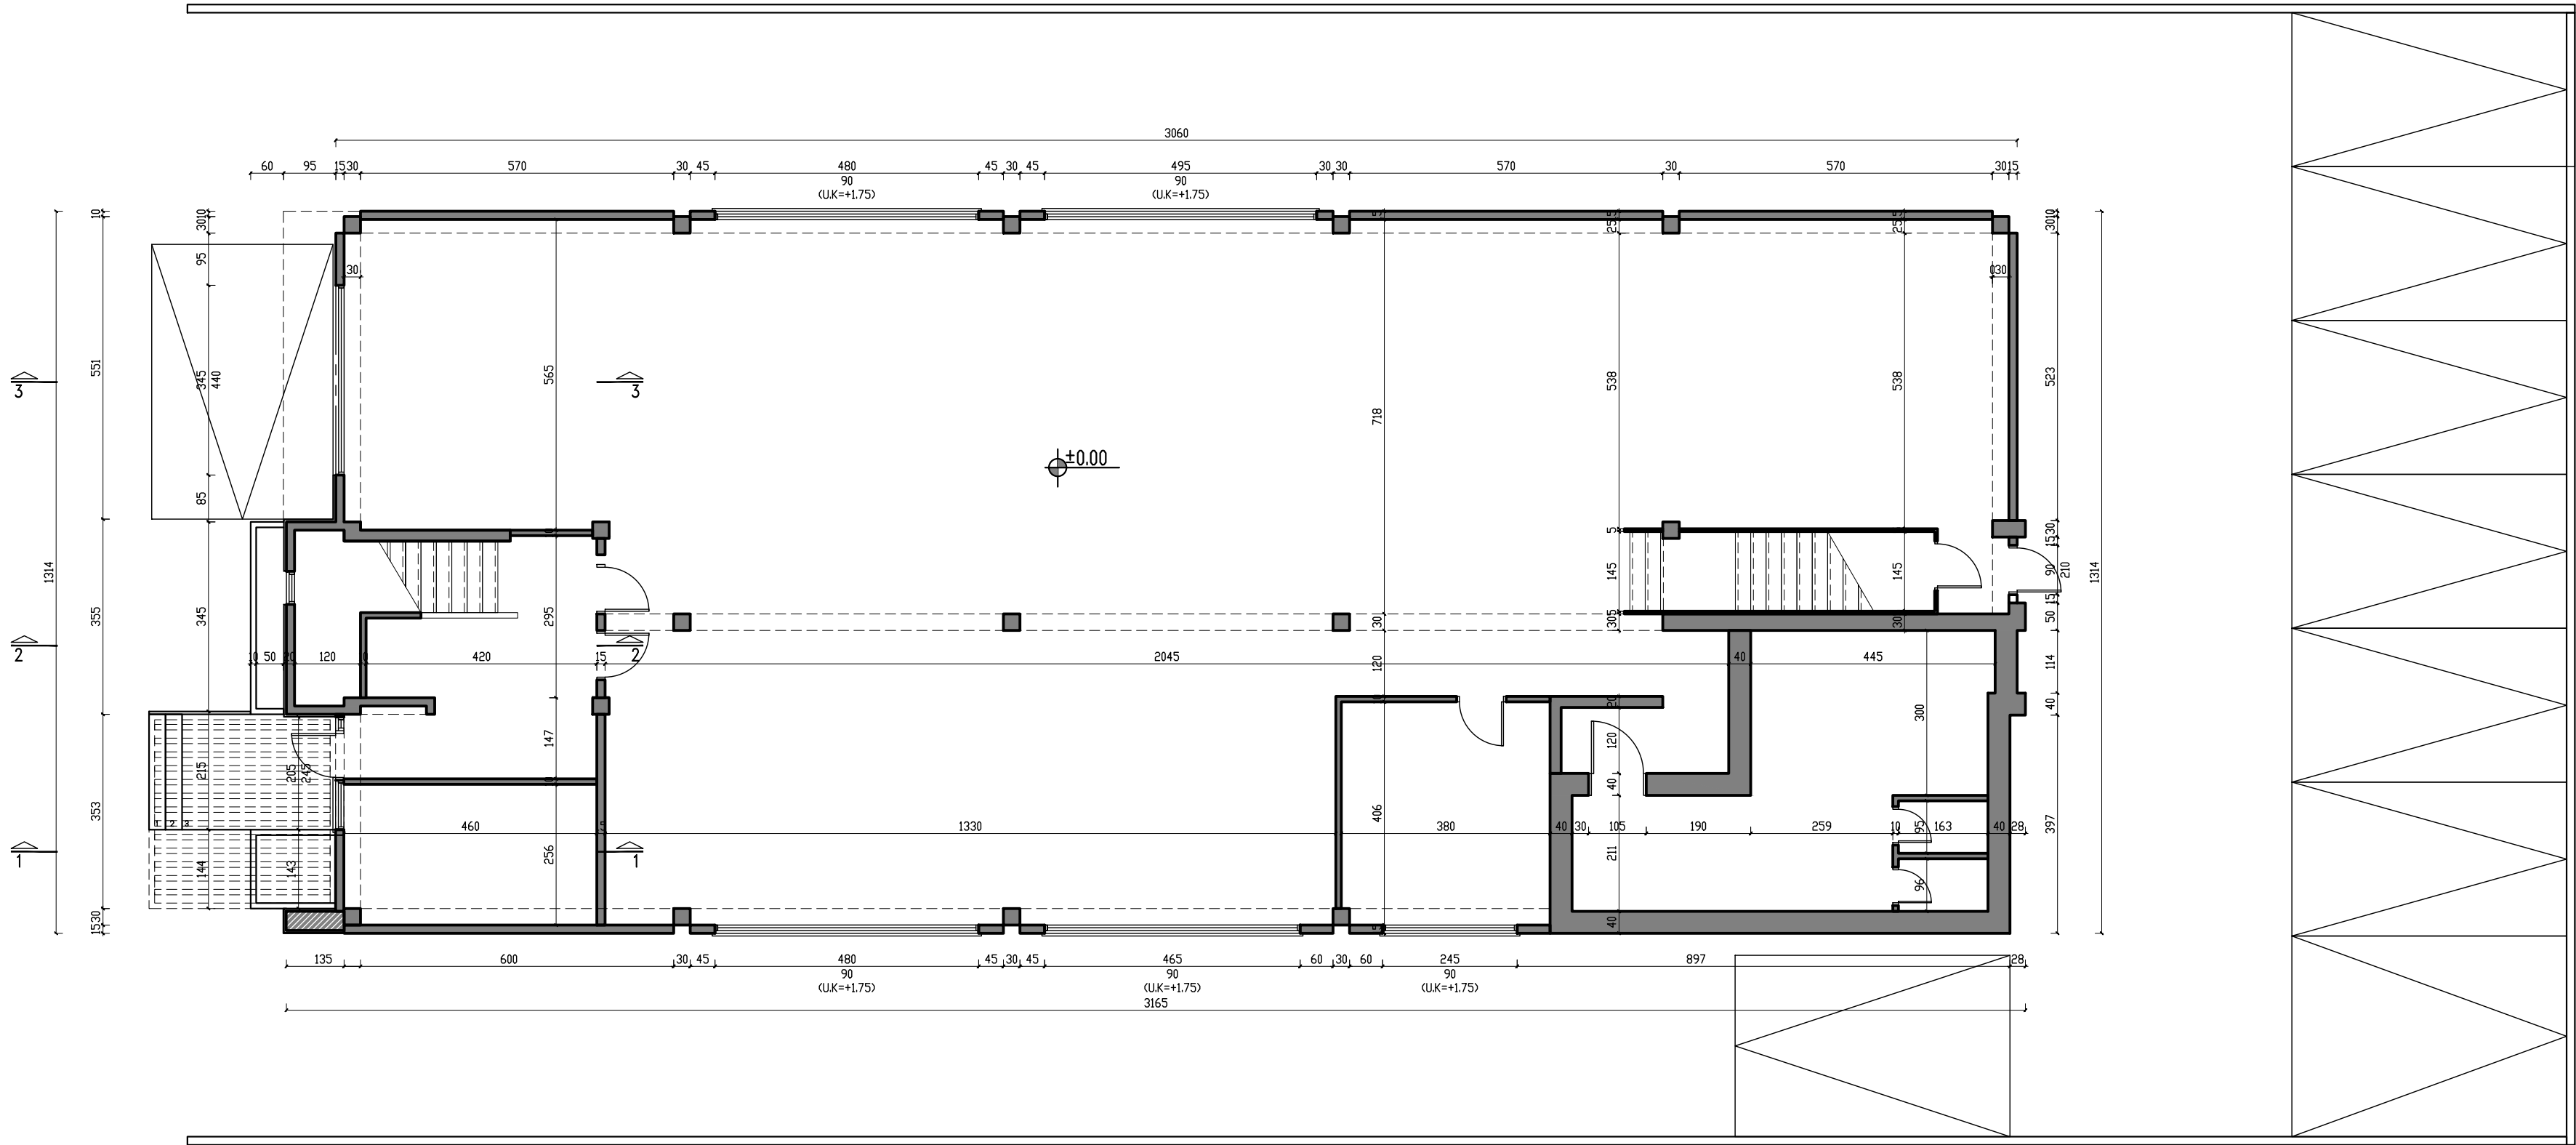

תכנית קומת קרקע

קני"מ 1:100
תכנית קומת קרקע
קני"מ 1:100

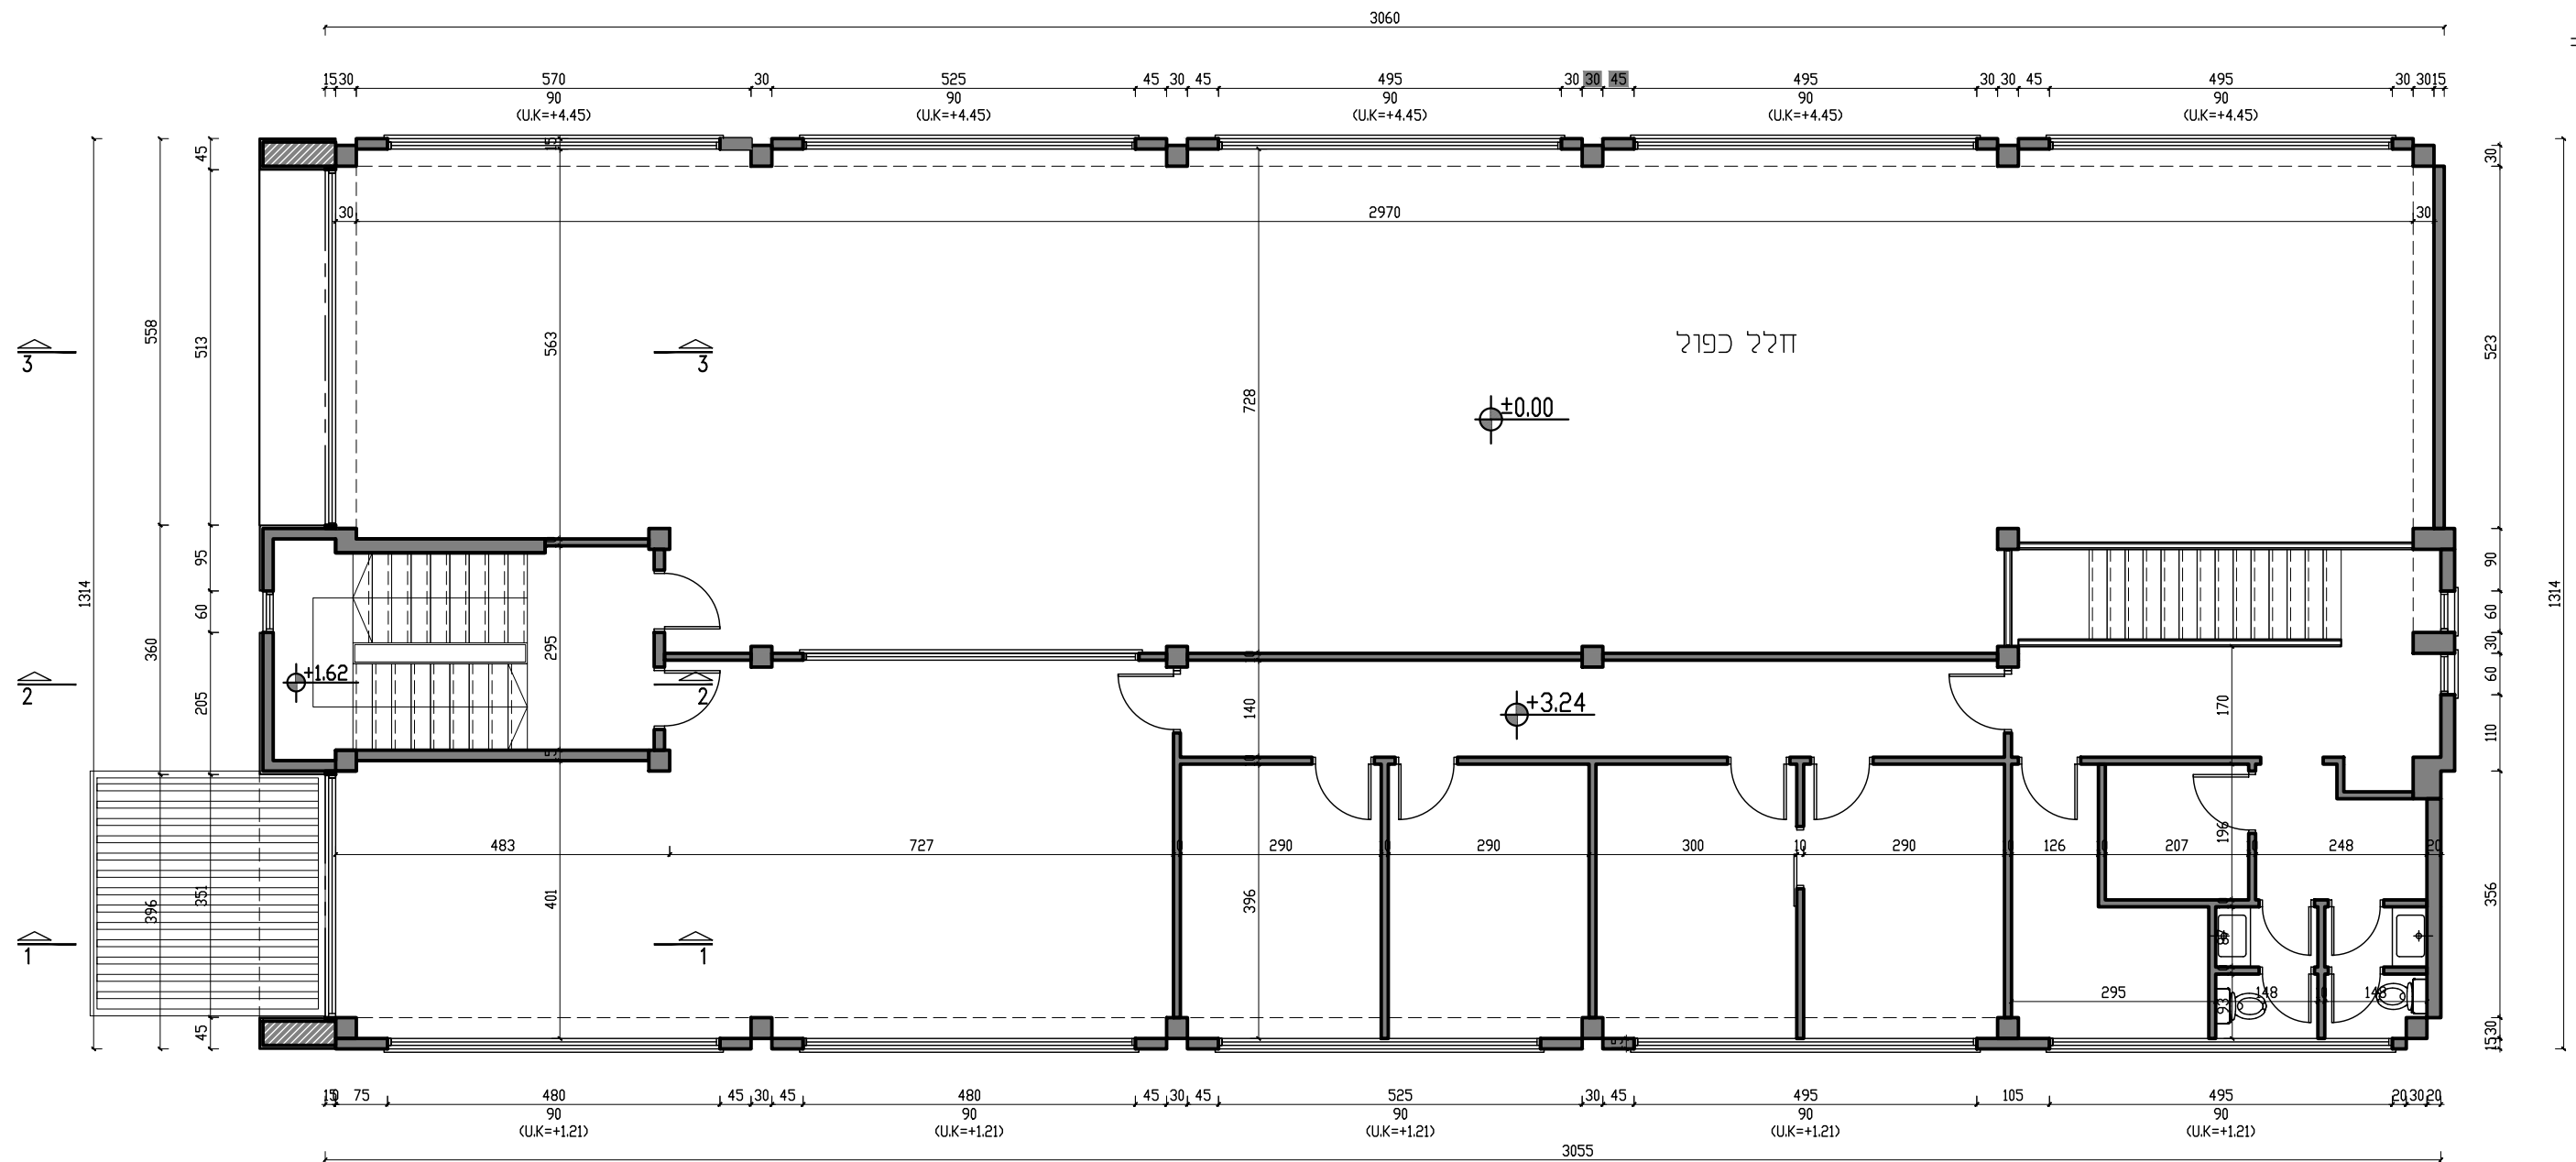

תכנית קומה א'

קני"מ 1:100