

מס', מהות העדכון	תאריך
1	
2	

רשימת תפוצה		מס'	תפקיד	שם	מס' תאריך	1	2	3	4	5	6
1	מזמין										
2	אדריכלות			אלכס ויסמן גדי ענבי							
3	קונסט'										
4	אינסטי'										
5	חשמל										
6	מודד										
7	קרקע										
8	קבלן										
	פיקוח - אתר -										

© כל זכויות שמורות למשרד ענבי ויסמן אדריכלים
הקבלן אחראי למידות, ועליו לבקר אותן ולהודיע למתכנן על כל
שעות, ססיה, סתירה או אי-התאמה בסרט ימשיך בעבודתו.
השימוש בתכנית זו רק בהסכמתו המפורשת של המתכנן.
אין לקבוע גדלים ע"י מדידה בשרטוט.

					מהדורה	
		4	1	2	2	
P	L	1	0	5		
שם התכנית:						
חתך 3-3						
+						
פרט 1 + פרט 2						
לביצוע					למכרז	
לאישר					1:50	
קנ"מ:						

תוכנן ע"י: אלכס ויסמן	בוקר ע"י: אלכס ויסמן
אדריכל אחראי במשרד: אלכס ויסמן	אושר ע"י: אלכס ויסמן
תאריך: 25.01.18	תאריך עדכון: 19.09.2022
שם וולונטר: 412-TRUFA-NETANYA.org	מידות גליון:
קבצים יש לשלוח לכתובת: alex@weismanarch.com	

תרופה , 4
נתניה






Weisman

Architects

וייסמן אדריכלים

מוריה 46, חיפה

052-3302396 אלכס

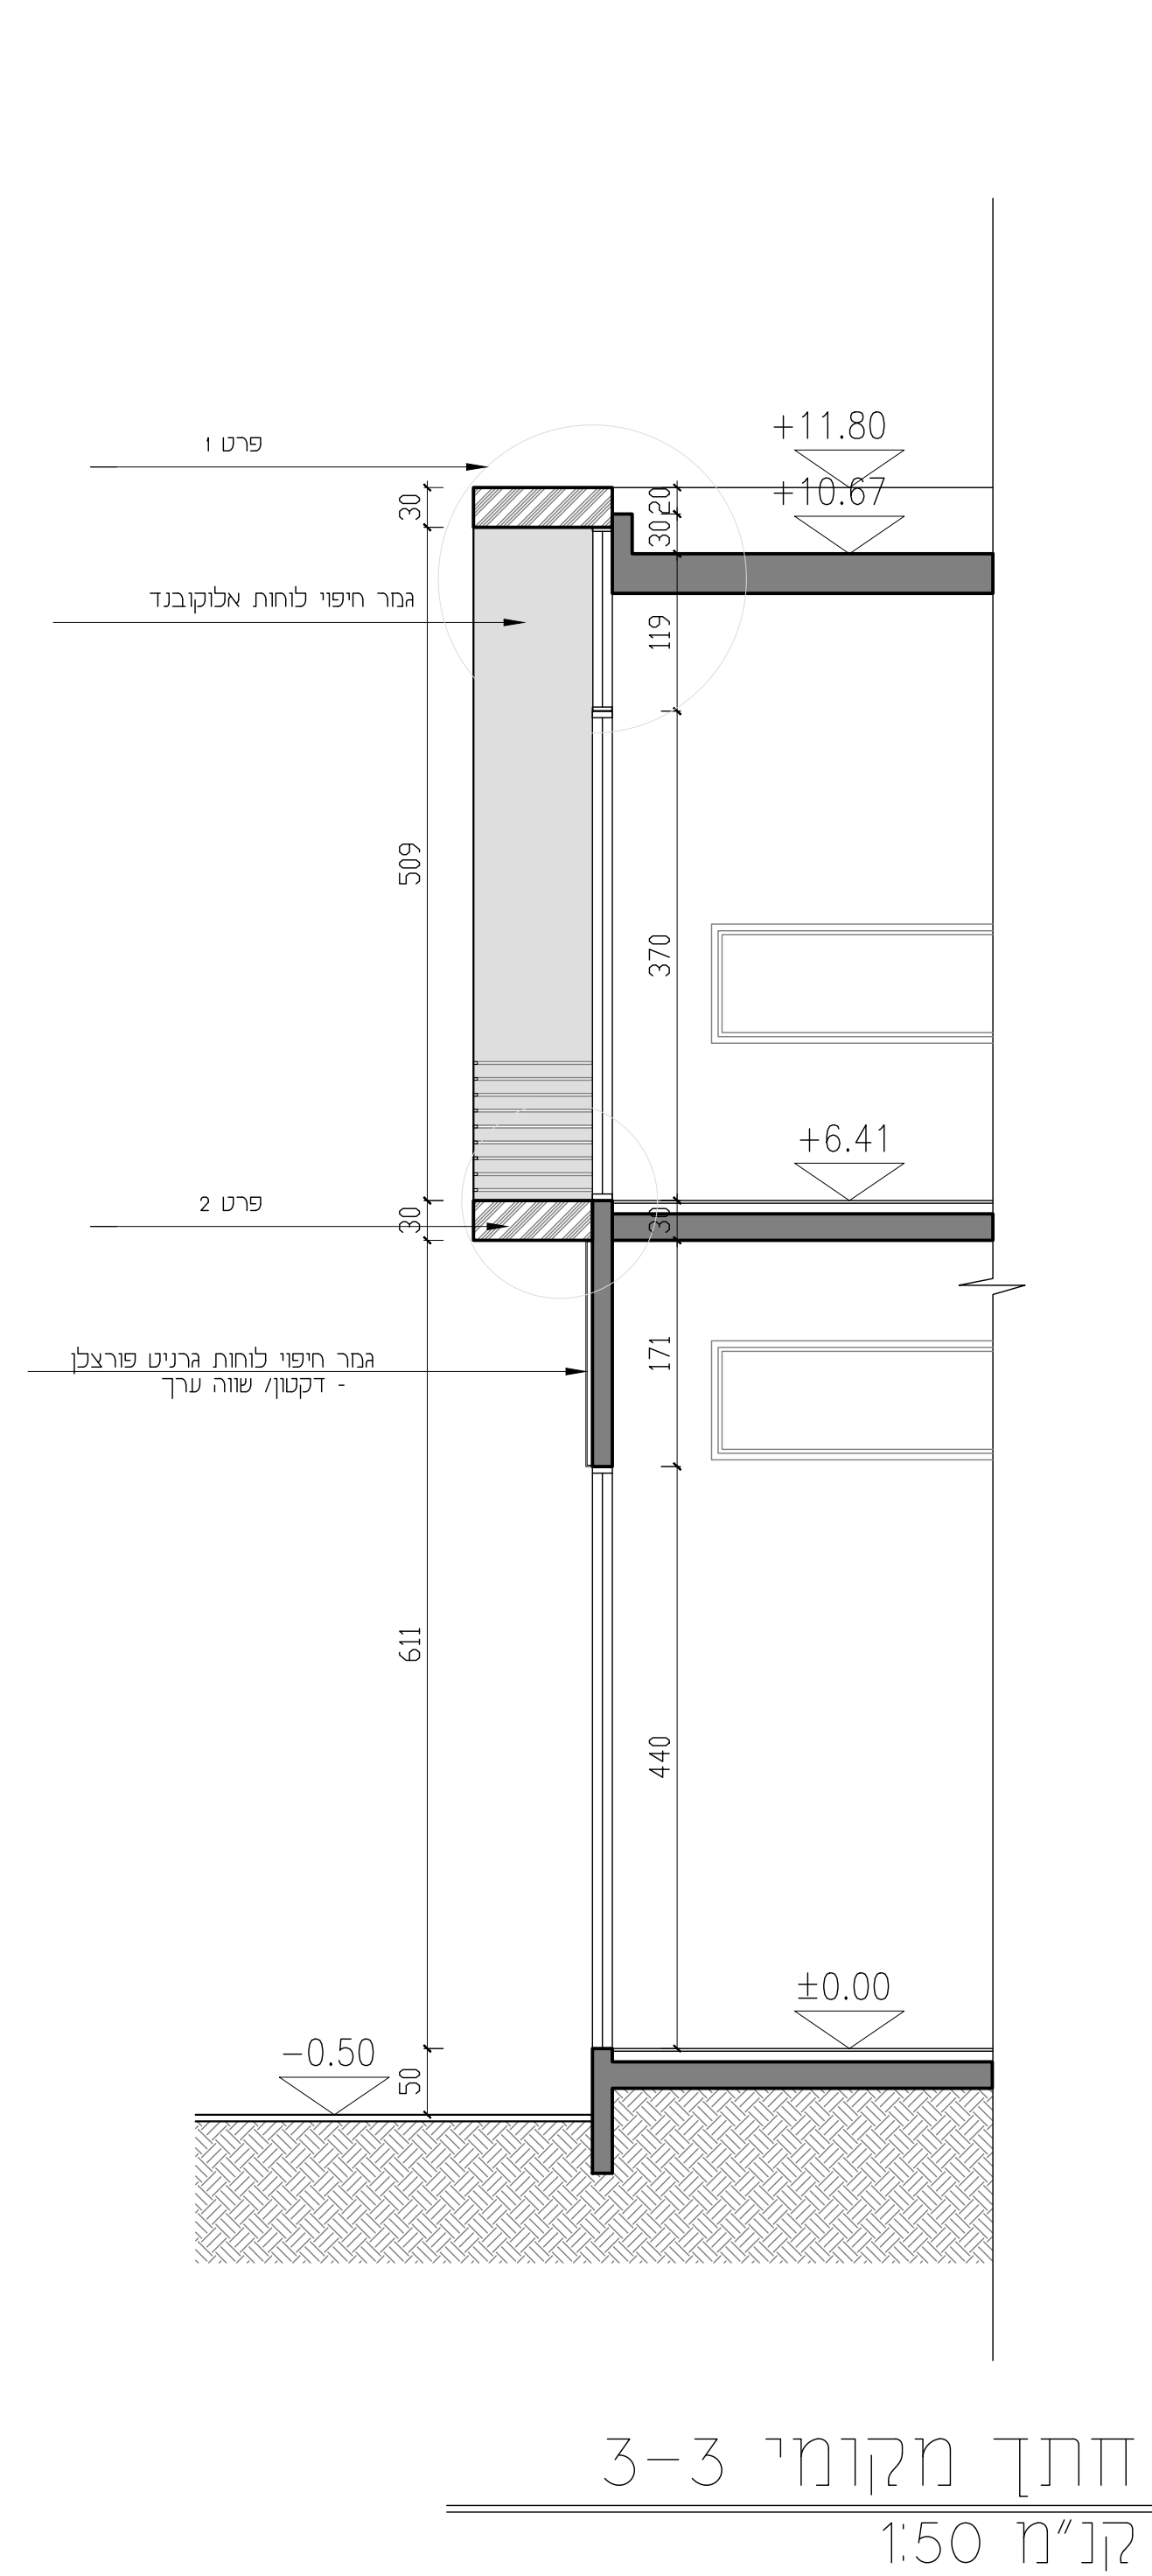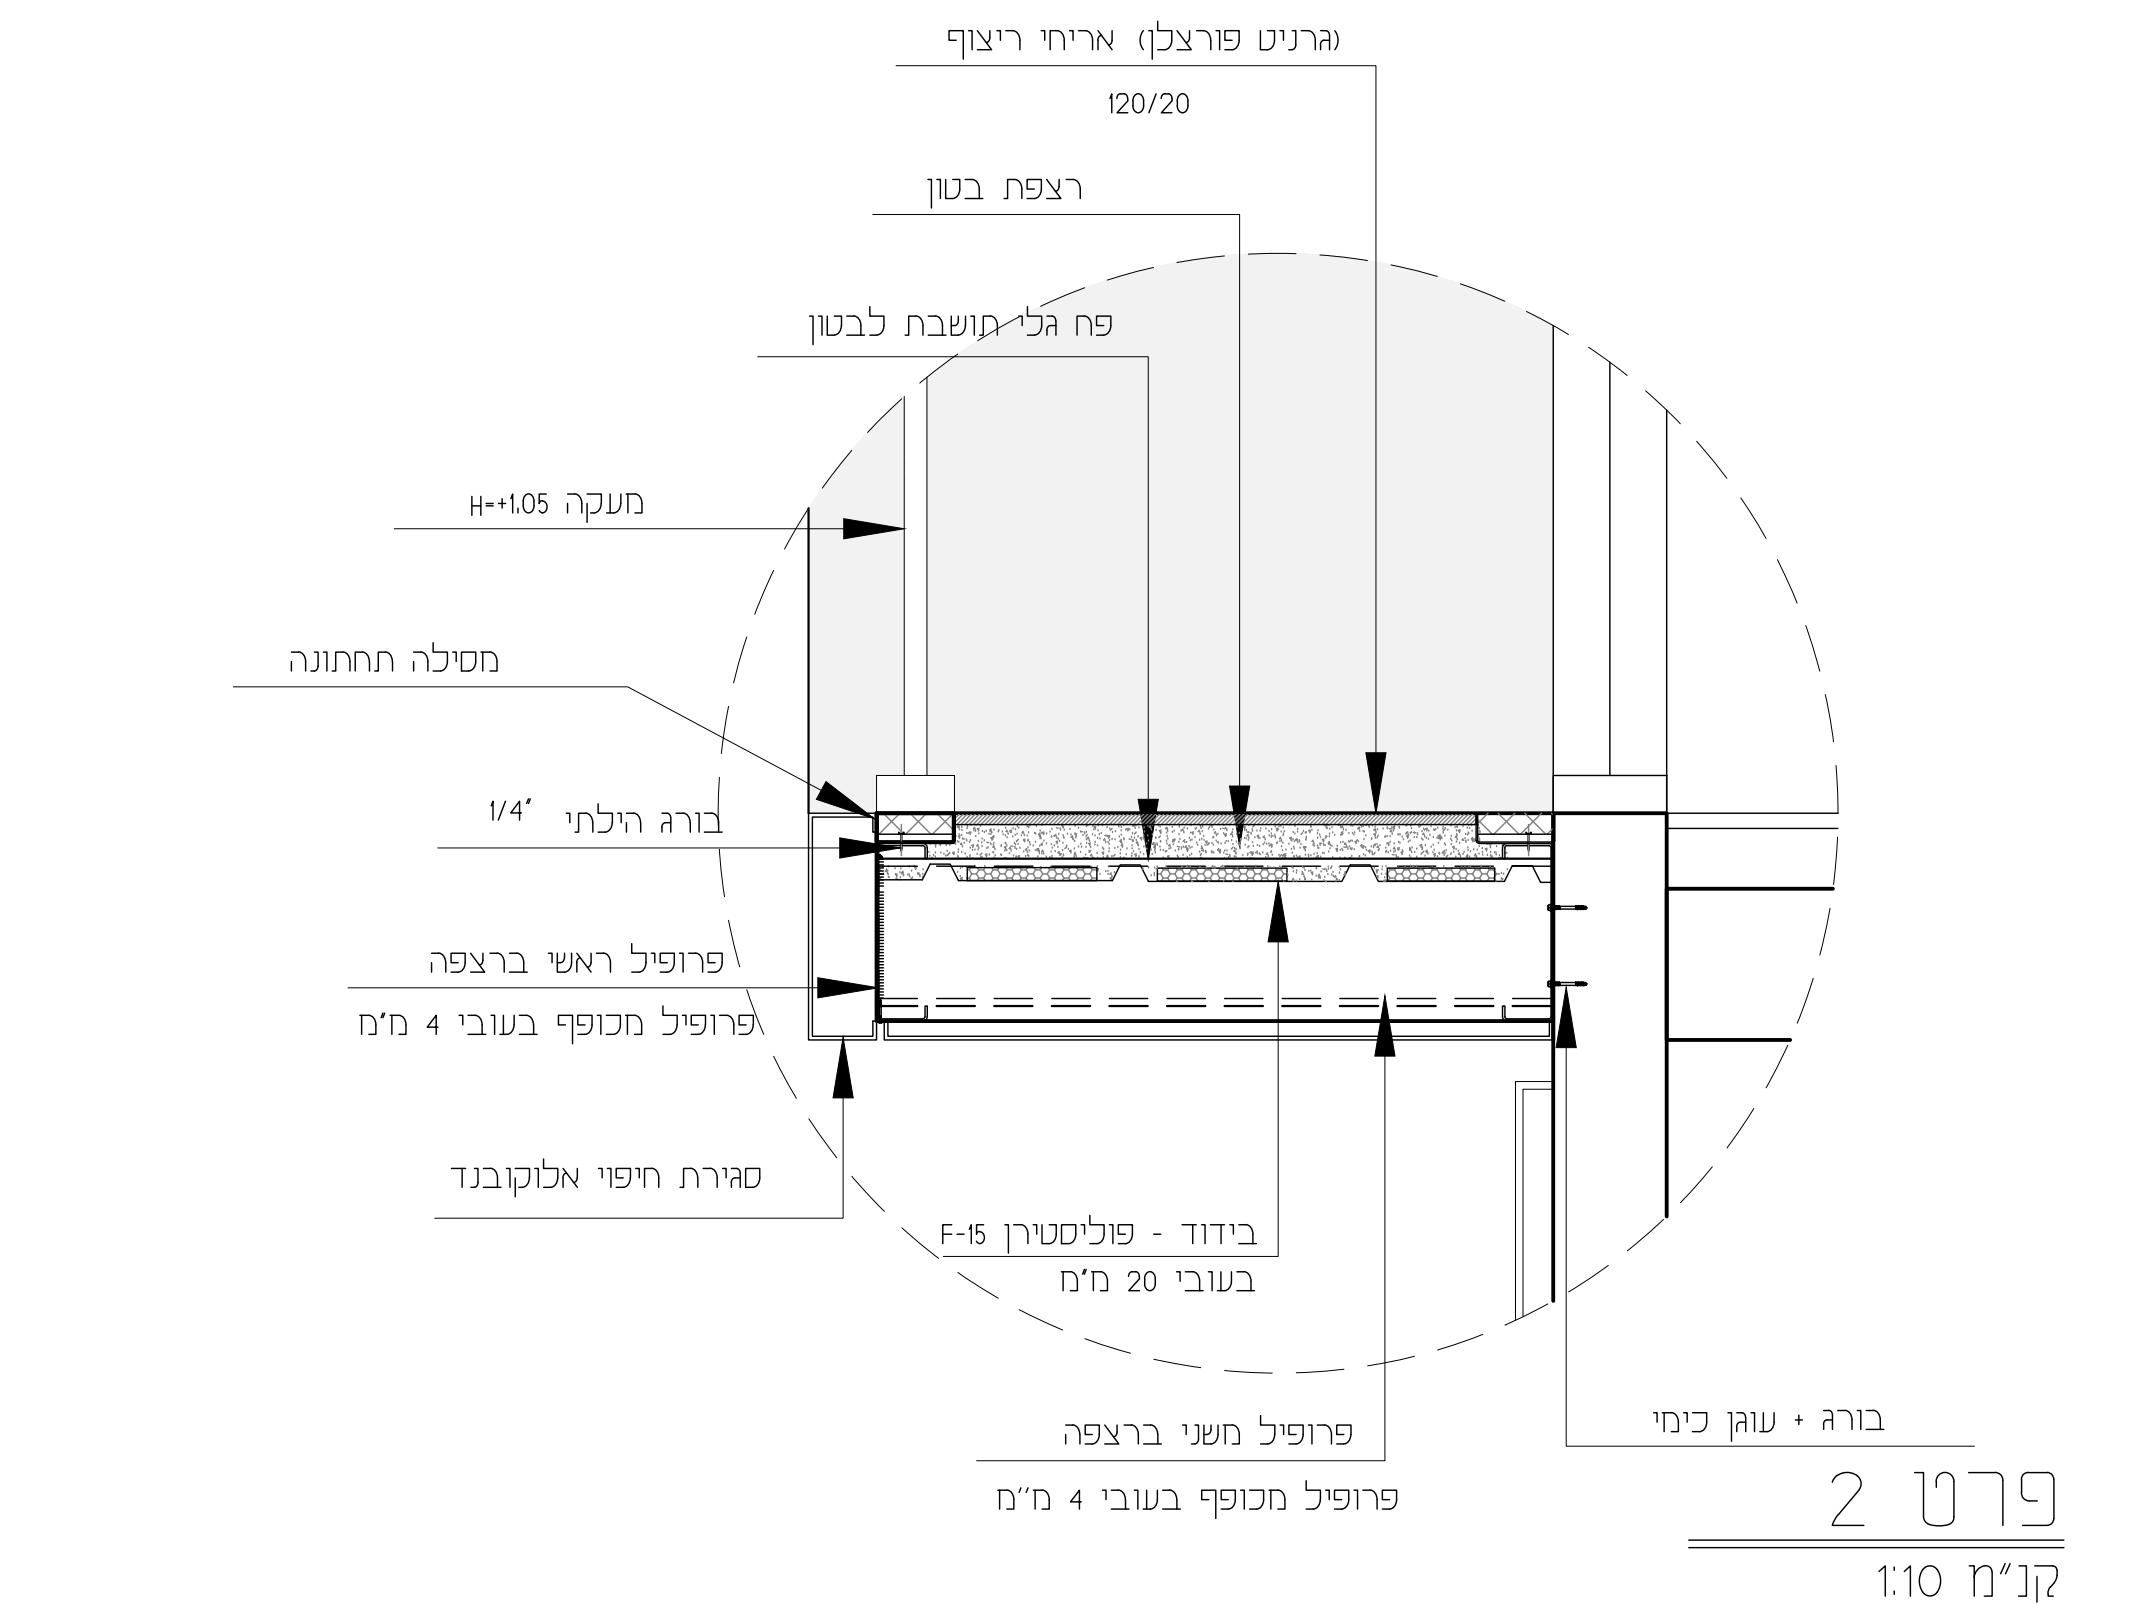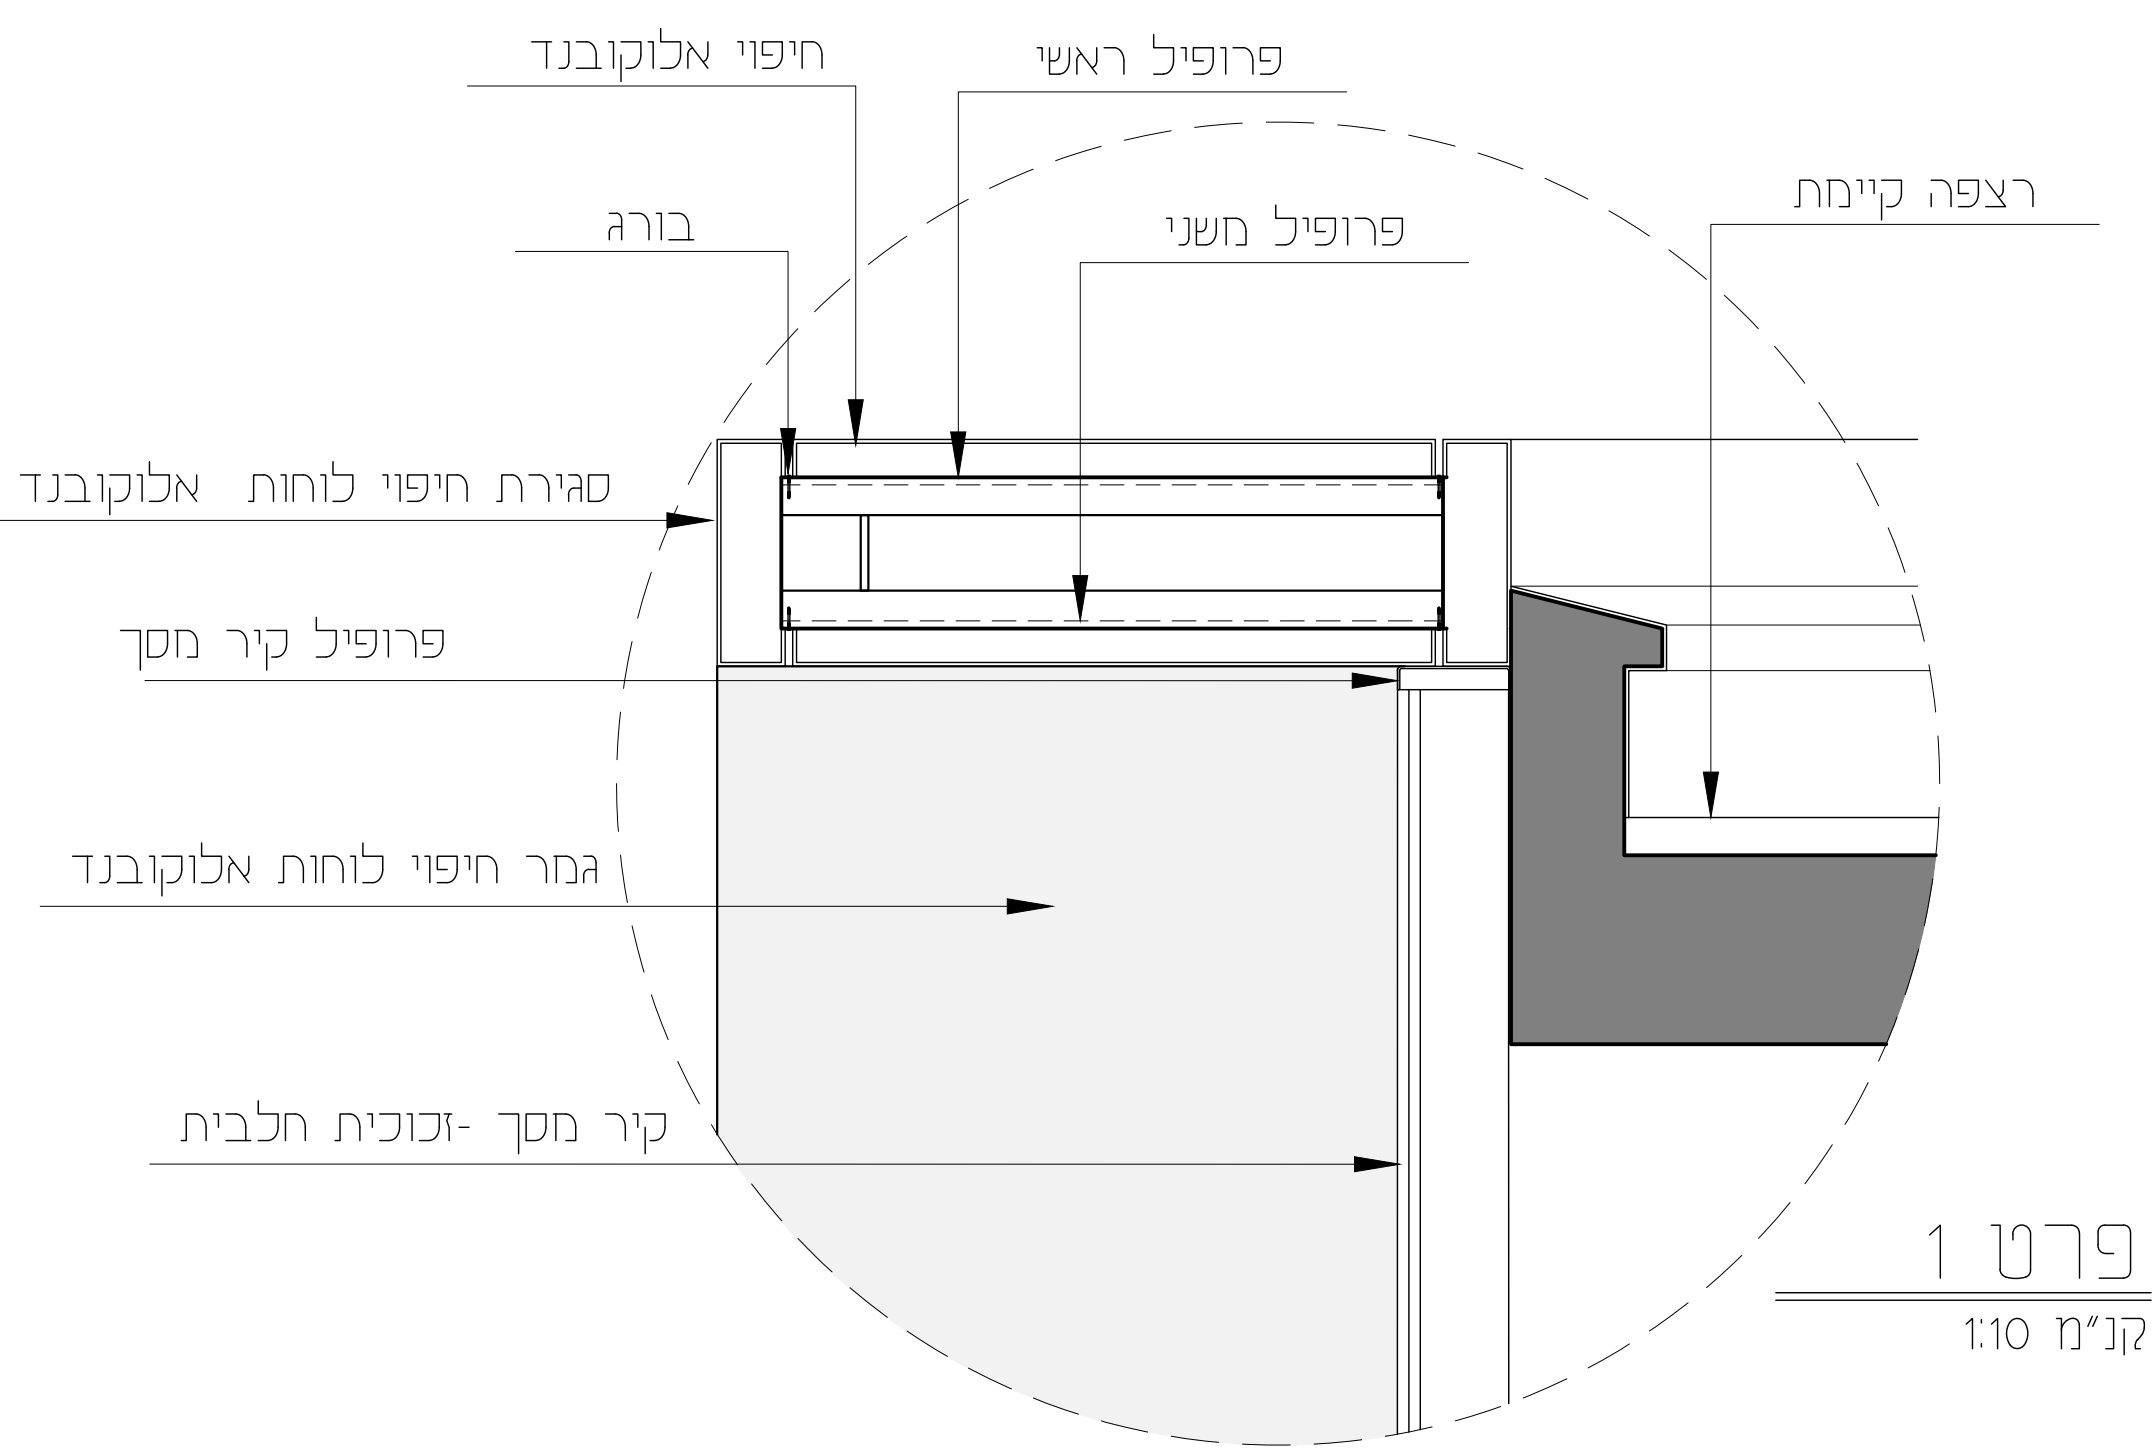



Weisman

Architects

וייסמן אדריכלים

מוריה 46, חיפה

052-3302396 אלכס