


קנ"מ:
1:50

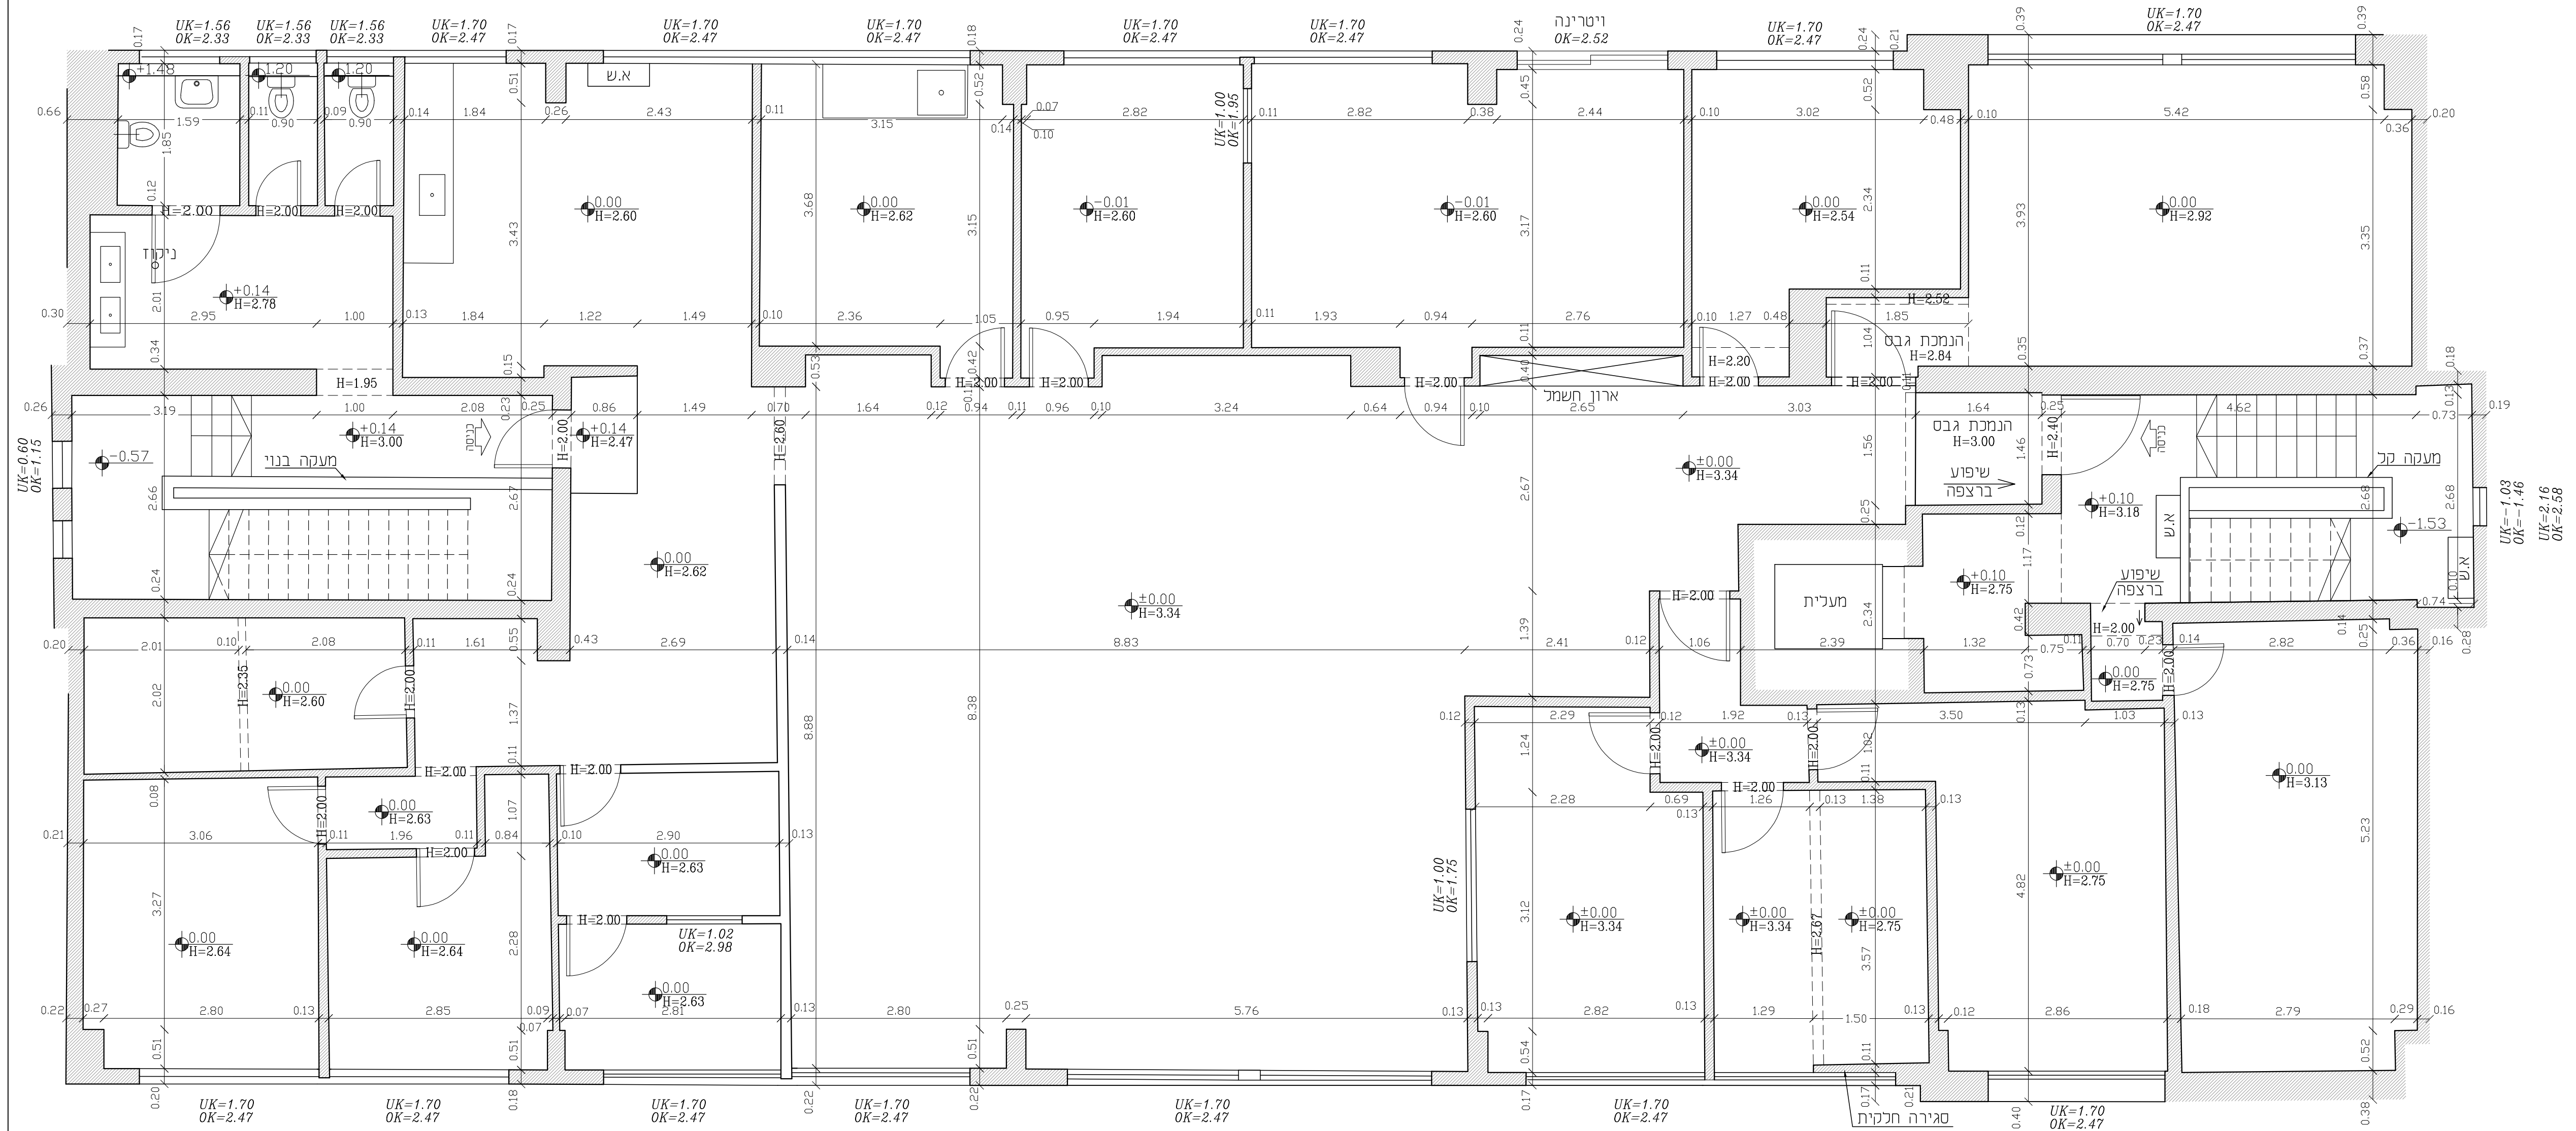

תאריך : 24.07.2025		שעות : מדינה	
דן שלינגר, מודד מוסמך, רישון מס 644		דן שלינגר, מודד מוסמך, רישון מס 1234	
שלינגר מדידות ומערכות מידע בל"מ		 ש"ל 03-9523332 רמת גן 4 office@dnts.co.il 24-07-2025 15:16 PNIN.dwg	

S:\2025\2025-0500\27732\27732-PNIM.dwg 24.07.2025 15:16 קובץ