


בית ספאר | אזה"ת בית ליד

PRION
BRODNER
ARCHITECTS



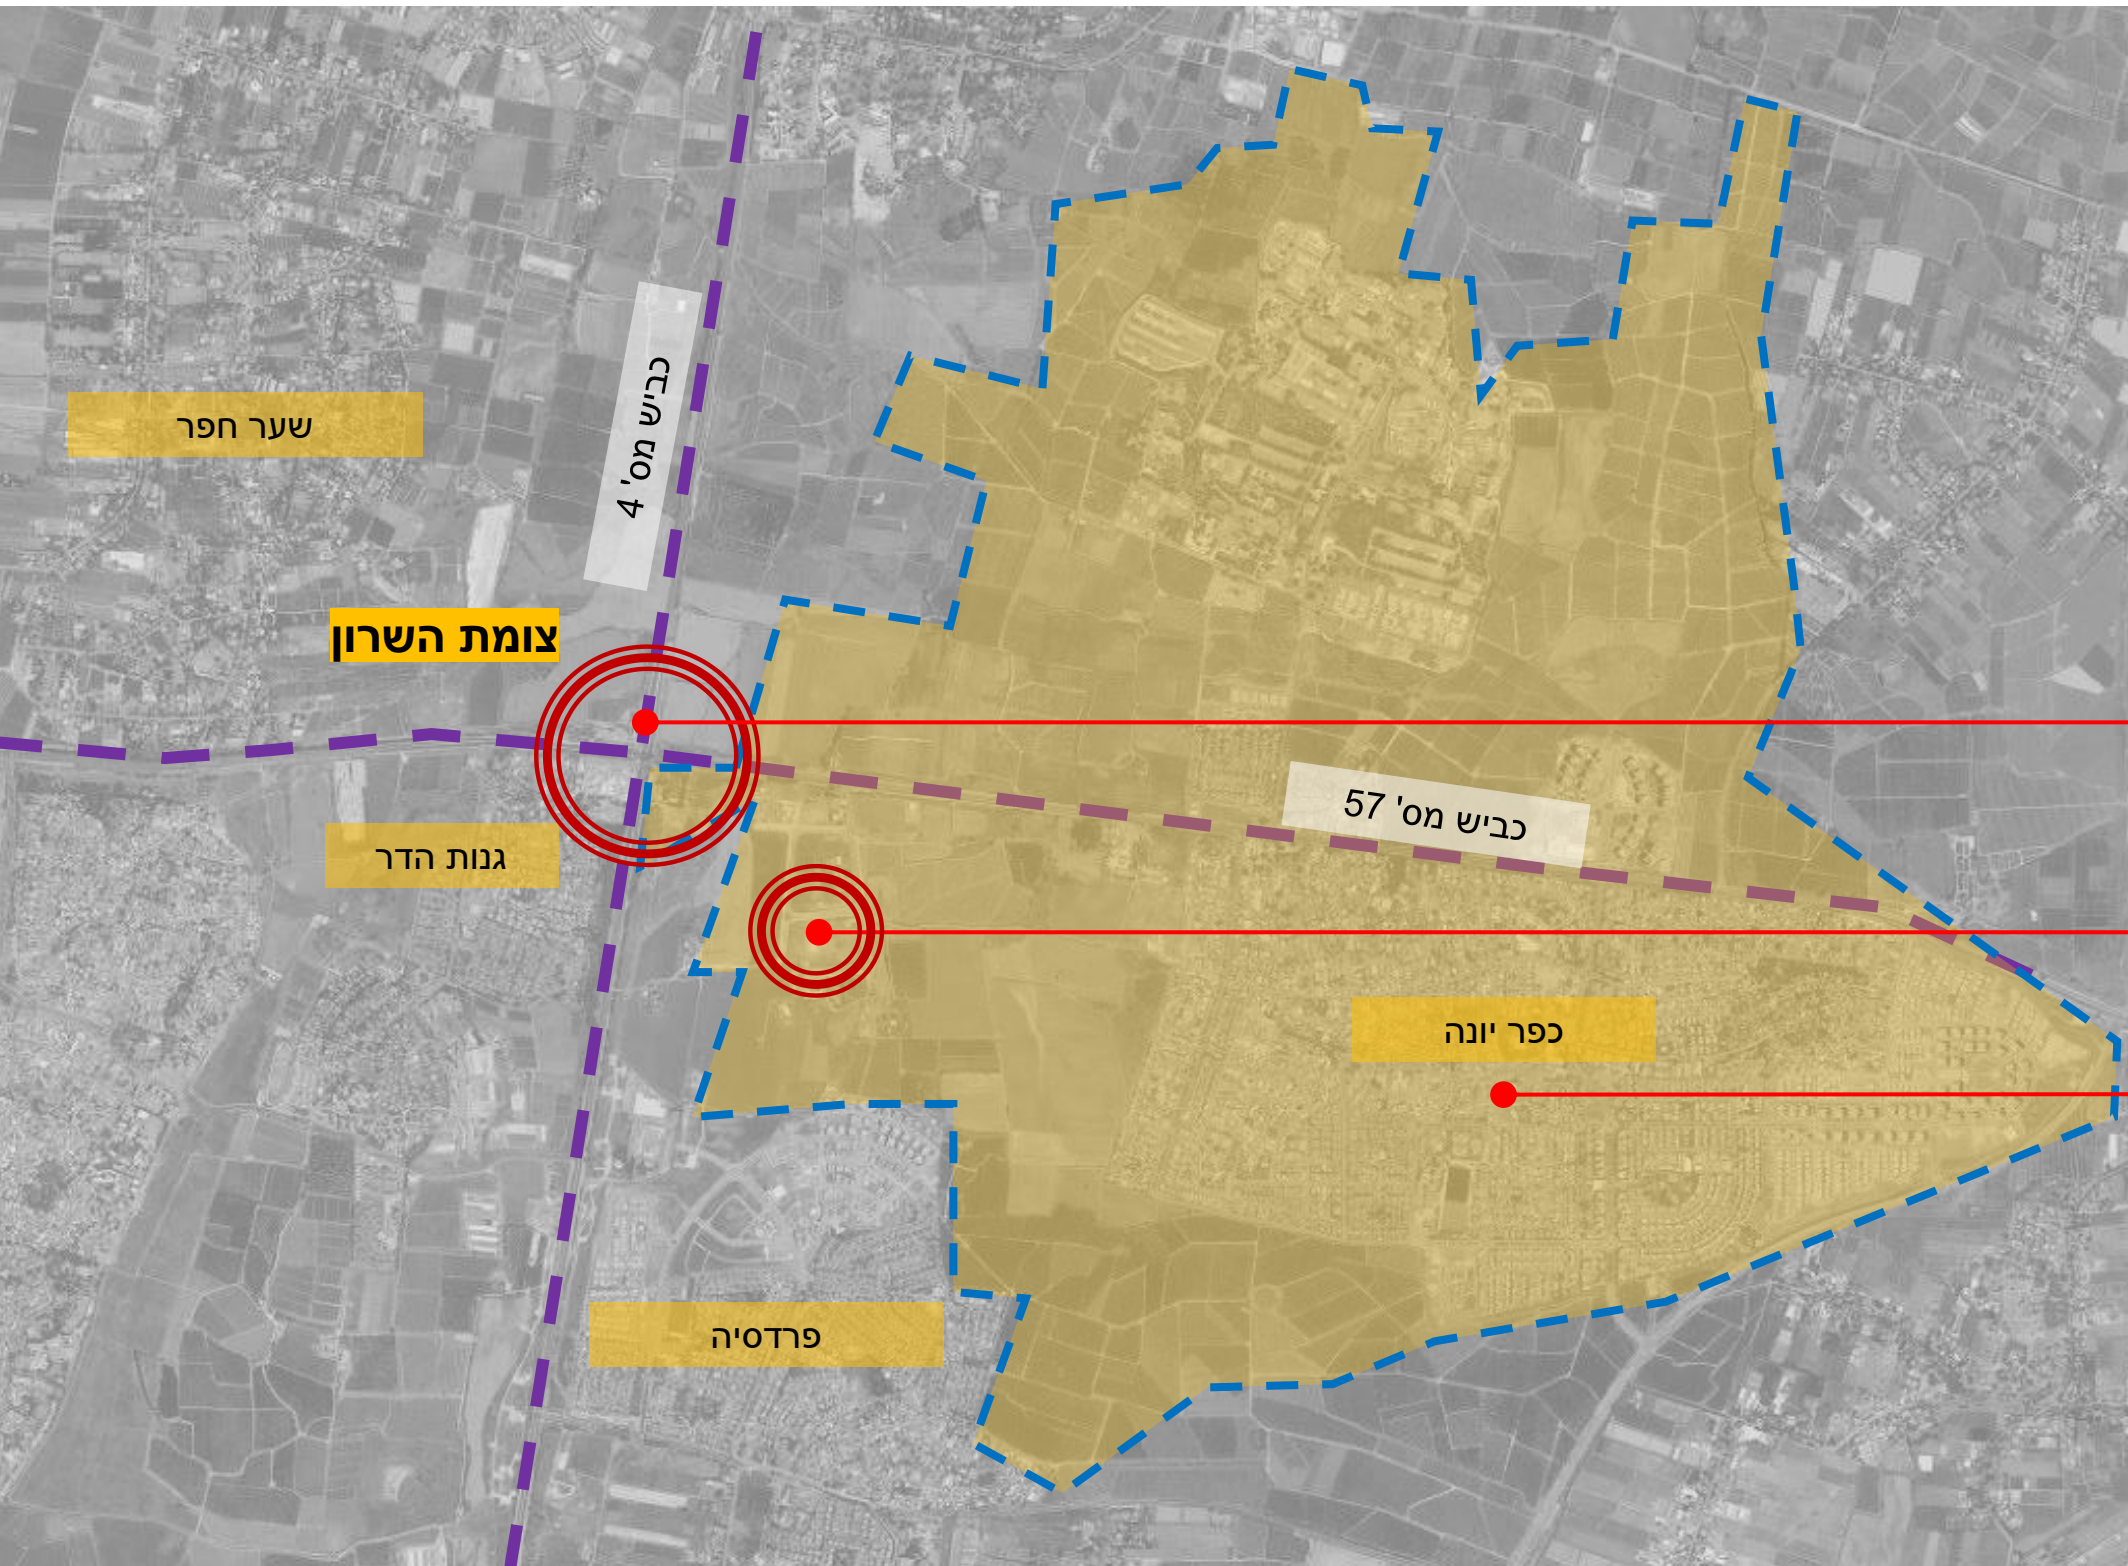

צומת השרון

אזה"ת בית ליד

אזור הפרויקט


כפר יונה

תחום מוניציפלי של הישוב

! שטח שיפוט – כ-11,500 דונם

! אוכלוסייה – כ-30,000 תושבים



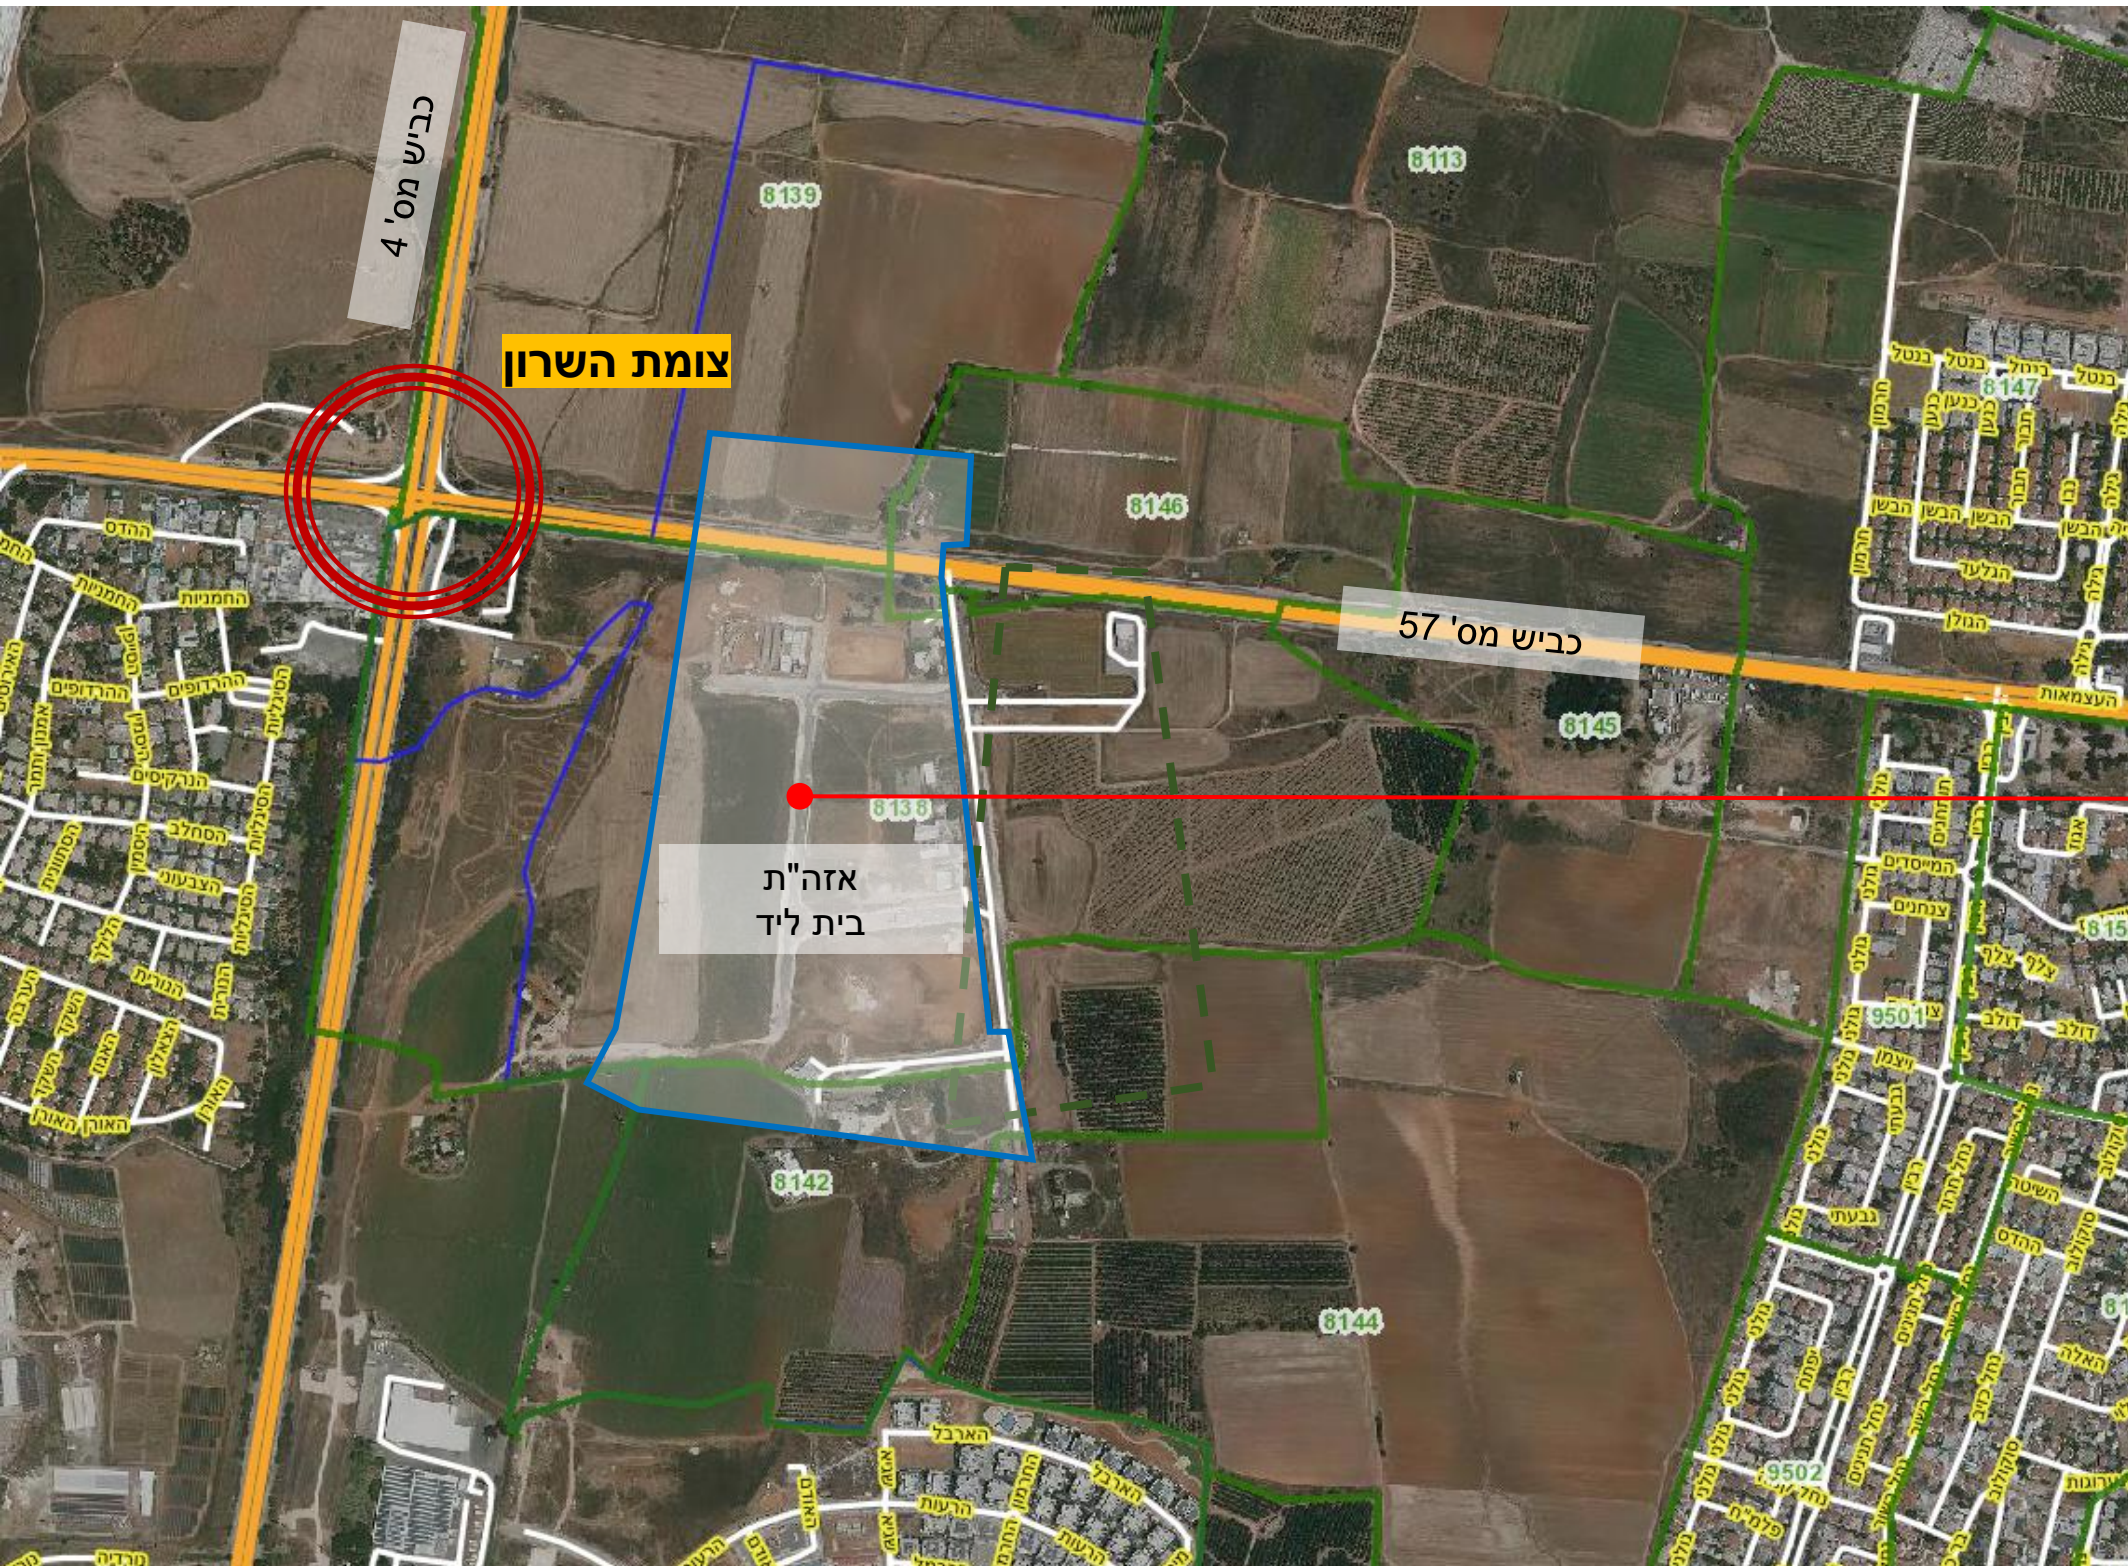

מיקום הפרויקט

אזור התעשייה בית ליד

תכנית בתוקף:

457-0284471



מיקום הפרויקט

גוש: 8138

חלקות: 205,177

מגרשים מס':

- 104 – 5.683 דונם
- 204 – 0.256 דונם
- 103 – 5.086 דונם
- 203 – 0.198 דונם
- סה"כ – 11.223 דונם

תכנית בתוקף:

457-0284471



גוש: 8138

חלקות:

מגרשים מס':

- 104 – 5.683 דונם
תעשייה
- 204 – 0.256 דונם
שפ"פ
- 103 – 5.086 דונם
תעשייה
- 203 – 0.198 דונם
שפ"פ
- סה"כ – 11.223 דונם

תכנית בתוקף:

457-0284471

תב"ע בתוקף
457-0284471

תוכנית מס' 457-0284471

עיקרי התוכנית:

- איחוד וחלוקה ללא הסכמת בעלים.
- שינוי מערך הדרכים, ביטול דרכים קיימות וקביעת דרכים חדשות.
- קביעת קווי בניין, גובהם של הבניינים ומספר הקומות.

מיקום הפרויקט

ייעוד: תעשייה

גוש: 8138

חלקות: 177,205

מגרשים מס':

- 104 – 5.683 דונם
- 204 – 0.256 דונם
- 103 – 5.086 דונם
- 203 – 0.198 דונם
- סה"כ – 11.223 דונם

תעשייה	
תעשייה קלה ומלאכה	
מבנים ומוסדות ציבור	
מבנים ומוסדות ציבור לחינוך	
שטח ציבורי פתוח	
שטח פרטי פתוח	



שימושים:

- מפעלים
- בית מלאכה
- משרדים
- מחסנים
- חנות לתצוגה

4.1	תעשיה
4.1.1	שימושים
*	א. בשטחים המיועדים לתעשייה יותרו אך ורק מפעלים לתעשייה בלתי מזיקה לסביבה.
	ב. כמו כן יותרו מתקני שירות למפעל כגון בית מלאכה, משרדים, מחסנים וכד', שמטרתם לשרת את יעוד המפעל. <u>תותר הקמת חנות לתצוגה ומכירה של מוצרי המפעל.</u>
	ג. תותר הקמת תחנת תדלוק עפ"י תכנית מפורטת מאושרת.
	ד. חניה - חניה עילית תהיה מגוננת נופית ובהתאם להנחיות תכנית הבינוי - בגבול תאי שטח ניתן לאשר רמפה ירידה למרתף חניה כזכות מעבר מוסכמת בין שני מגרשים.

ז. חניה - חניה עילית תהיה מגוננת נופית ובהתאם להנחיות תכנית הבינוי - בגבול תאי שטח ניתן לאשר רמפה ירידה למרתף חניה כזכות מעבר מוסכמת בין שני מגרשים.

תכנית מס': 457-0284471 - שם התכנית: אזה"ת בית ליד, איחוד וחלוקה, הצ/מק/1-2/258

תעשיה	4.1
ובהתאם להנחיות נספח הנוף. י. בטרם קבלת היתר בניה יתואמו השימושים על-פי תכנית זו עם הרשות מקומית ו/או מנהלת אזור התעסוקה. יא. במגרשים בהם קיים שטח פרטי פתוח לחזית הרחוב ישמש שטח זה למעבר תשתיות, חנייה, הולכי רגל, משטחים מרוצפים וקולונאדות בהתאם להוראות תכנית זו ותכנית הבנוי שתאושר. יב. קומת מרתף : ניתן יהיה לבנות קומת מרתף בקנטור המגרש - יישמר קו הבניה הקדמי ללא מרתף למעט ירידה לרכב. קומת המרתף תשמש לחניה, לחדרי עזר וחדרים לשירותים הנדסיים לבניין, לאחסנה, למרחבים מוגנים וכדומה. גובה קומת המרתף יהיה 3.5 מטרים כולל מערכות נדרשות לכלל הבניין. קומת המרתף תהיה חלק בלתי נפרד מהמבנה שמעליה (לא כיחידה נפרדת). יש לתת פתרון בקומת המרתף לאור טבעי ואורור. 10% מגובה הקומה יכול להיות מעל פני הקרקע, ובלבד שגובה המבנה לא יעלה על סה"כ הגובה המותר. שטח קומת המרתף בהתאם למצוין בטבלת הזכויות לא יעלה על 80% משטח המגרש (לצורך שמירת 20% משטח הקרקע פנויה לגר עילי). יג. למגרש בו יבוצעו 80% מהחניות במרתף תוגדל התכסית ל-55%. יד. בכל עסקי המזון תחויב הרחקת אדים וריחות באמצעות פירים שקצה ארובתם יהיה מעל הגג העליון ושאינם חשופים לחזית הרחוב.	

גוש: 8138

חלקות: 177,205

מגרשים מס':

- 104 – 5.683 דונם
- 204 – 0.256 דונם
- 103 – 5.086 דונם
- 203 – 0.198 דונם
- סה"כ – 11.223 דונם

גוש: 8138

חלקות: 177,205

מגרשים מס':

- 104 – 5.683 דונם
- 204 – 0.256 דונם
- 103 – 5.086 דונם
- 203 – 0.198 דונם
- סה"כ – 11.223 דונם

5. טבלת זכויות והוראות בניה - מצב מוצע

קו בנין (מטר)	מספר קומות	גובה מבנה- מעל הכניסה הקובעת (מטר)	מספר יח"ד	תכנית (% מתא שטח)	שטחי בניה (מ"ר)				גודל מגרש (מ"ר)	תאי שטח	יעוד		
					מעל הכניסה הקובעת		מתחת לכניסה הקובעת						
					עיקרי	שרות	עיקרי	שרות					
קדמי	אחורי	צידי-ימני	צידי-שמאלי	מעל הקובעת					גודל מגרש כללי				
5	5 (4)	5 (4)	5 (4)	3	12 (3)	45			25%	120 (2)	(1)	100 - 114, 116 - 212, 213	תעשייה
(5)	(5)	(5)	(5)	3	12	45			25%	120 (2)	(1)	117 - 121	תעשייה קלה ומלאכה
5 (7)	5 (7)	4 (6)	4 (6)	3	12	40			40%	120%	(1)	62 - 63	מסחר ומשרדים
5 (7)	5 (7)	5 (7)	5 (7)	4	16	30 (9)				120 (8)	(1)	1 - 3	מבנים ומוסדות ציבור
(10)	(10)	(10)	(10)								(1)	4	מבנים ומוסדות ציבור לחינוך

הערה ברמת הטבלה:

- א. שטחי שירות בקומת המרתף בכל תחום התכנית - בהתאם לתכנית המרתפים הצ/1-2/100א'.
- ב. לתאי השטח בייעוד - תעשייה - סככות חניה ו/או אחסנה כלולות במנין שטחי השירות.

הערות לטבלת זכויות והוראות בניה – מצב מוצע:

- (1) כמסומן בתשריט.
- (2) הערך מתייחס ל% מתא שטח, הערה: כולל שטחי הגלריות.
- (3) לא כולל מתקנים על הגג.
- (4) לסככת חניה או אחסנה גם 0.0 בהסכמת השכן הגובל.

גוש: 8138

חלקות: 177,205

מגרשים מס':

- 104 – 5.683 דונם
- 204 – 0.256 דונם
- 103 – 5.086 דונם
- 203 – 0.198 דונם
- סה"כ – 11.223 דונם

תעשייה	ייעוד
8138	גוש
205	חלקה
104	מגרש
5683	שטח מגרש

תעשייה	ייעוד
8138	גוש
177	חלקה
103	מגרש
5086	שטח מגרש

10769	סה"כ שטח שני המגרשים
-------	----------------------

• זכויות בניה על קרקעיות:

מ"ר	%	
12922.8	120%	שטח עיקרי
2692.25	25%	שטח שירות
15615.05		סה"כ זכויות בניה על קרקעיות

זכויות תת קרקעיות: 6173 (תכסית קומת קרקע) $3 \times 18519 <$ מ"ר

• הוראות נוספות:

➤ מס' קומות: 3

➤ גובה מותר – 12 מ'

➤ תכסית מותרת 45% - 5051 מ"ר

➤ ע"פ התב"ע, למגרש בו יבוצעו 80% מהחניות במרתף תוגדל התכסית ל-55% $6173 <$ מ"ר

תכנון מוצע

על קרקעי

- קומת קרקע מסחרית הכוללת:
 - ✓ סופר בשטח של 3000 מ"ר (של חברת ספאר).
 - ✓ אולמות תצוגה ושטחי מסחר
 - ✓ לובי + גרעין לבניין משרדים – עתידי.
- קומה 1 - אחסנה לוגיסטית בשטח של כ-6300 מ"ר (עבור חברת ספאר, בגובה של 12 מ') + 1000 מ"ר משרדים.
- שלב ב (לאחר אישור תכנית המתאר החדשה) - 4 קומות משרדים


תת קרקעי

- חניונים תת קרקעיים (כוללים הכנה לזכויות ושימושים עתידיים).
- אחסנה לוגיסטית תת קרקעית בשטח של כ-2000 מ"ר

שלב א':




שלב ב':

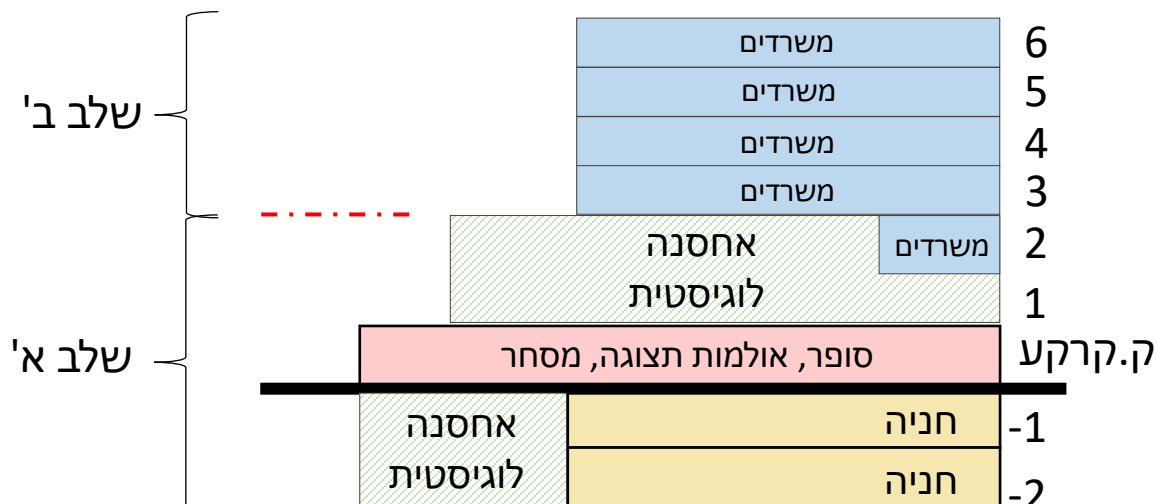





מגרשים 103+104

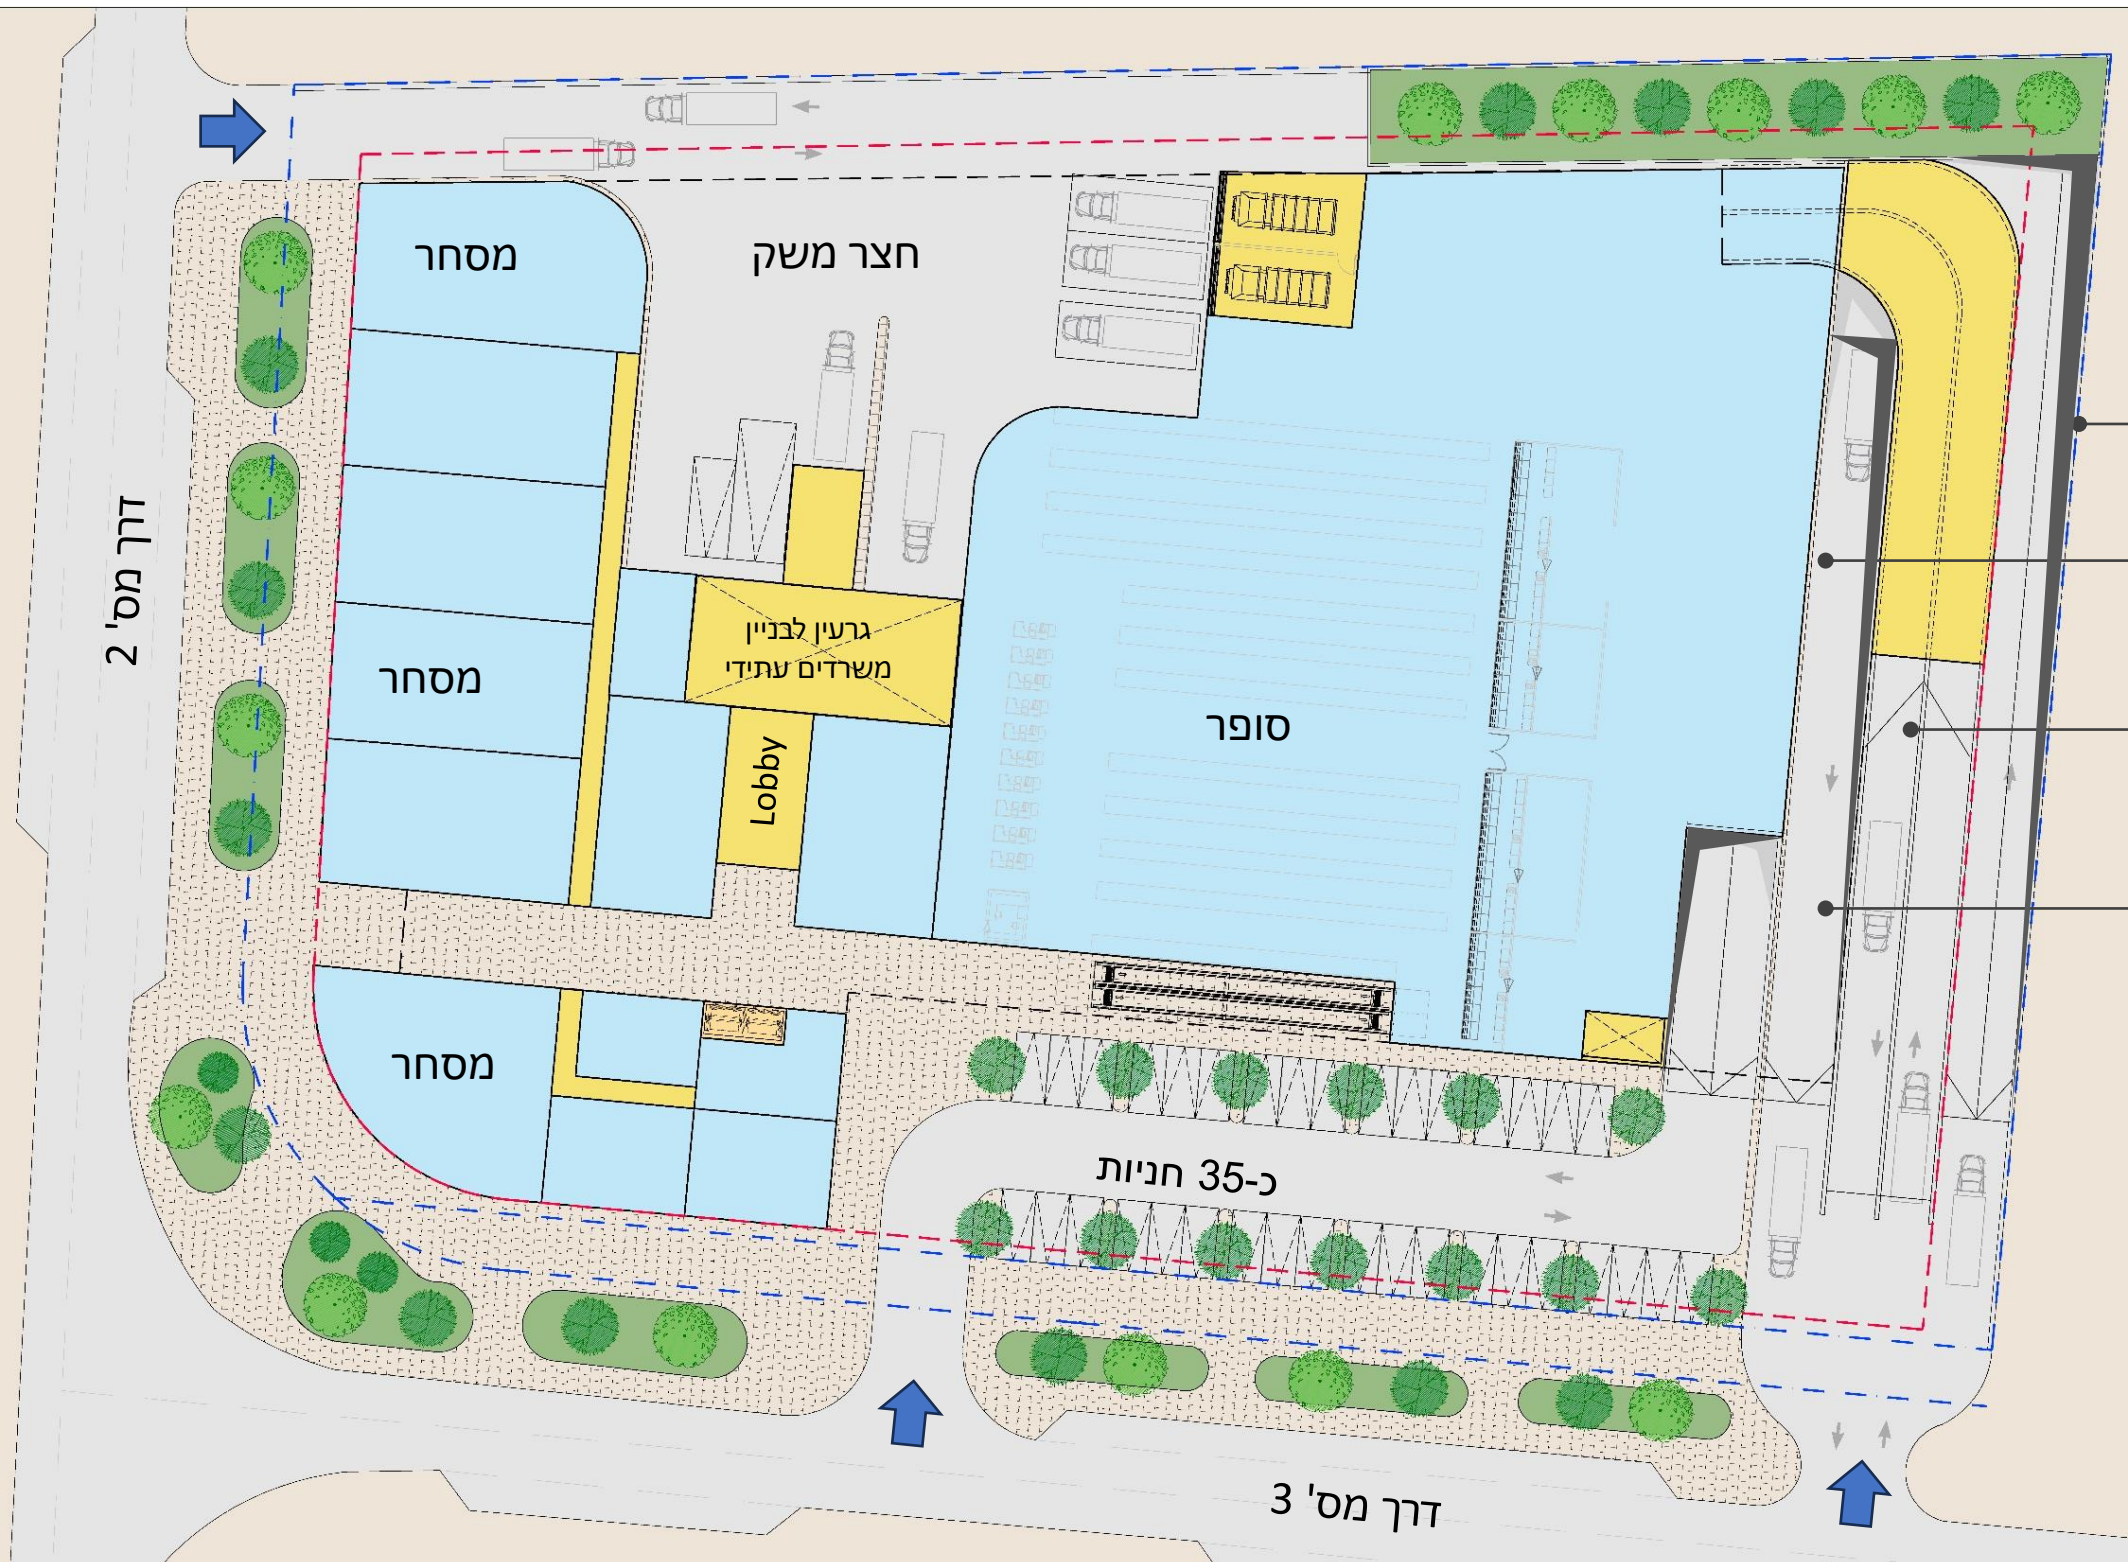

רמפת ירידה למרתף
למשאיות (לוגיסטיקה)

רמפת עליה ממרתף
למשאיות (לוגיסטיקה)


רמפת עליה לקומה
לקומה לוגיסטית 1

רמפת ירידה
לרכבים פרטיים

מסחר

גרעינים, טכני

- שטח קומה ברוטו:
כ-7000 מ"ר
- תכסית - כ-65%

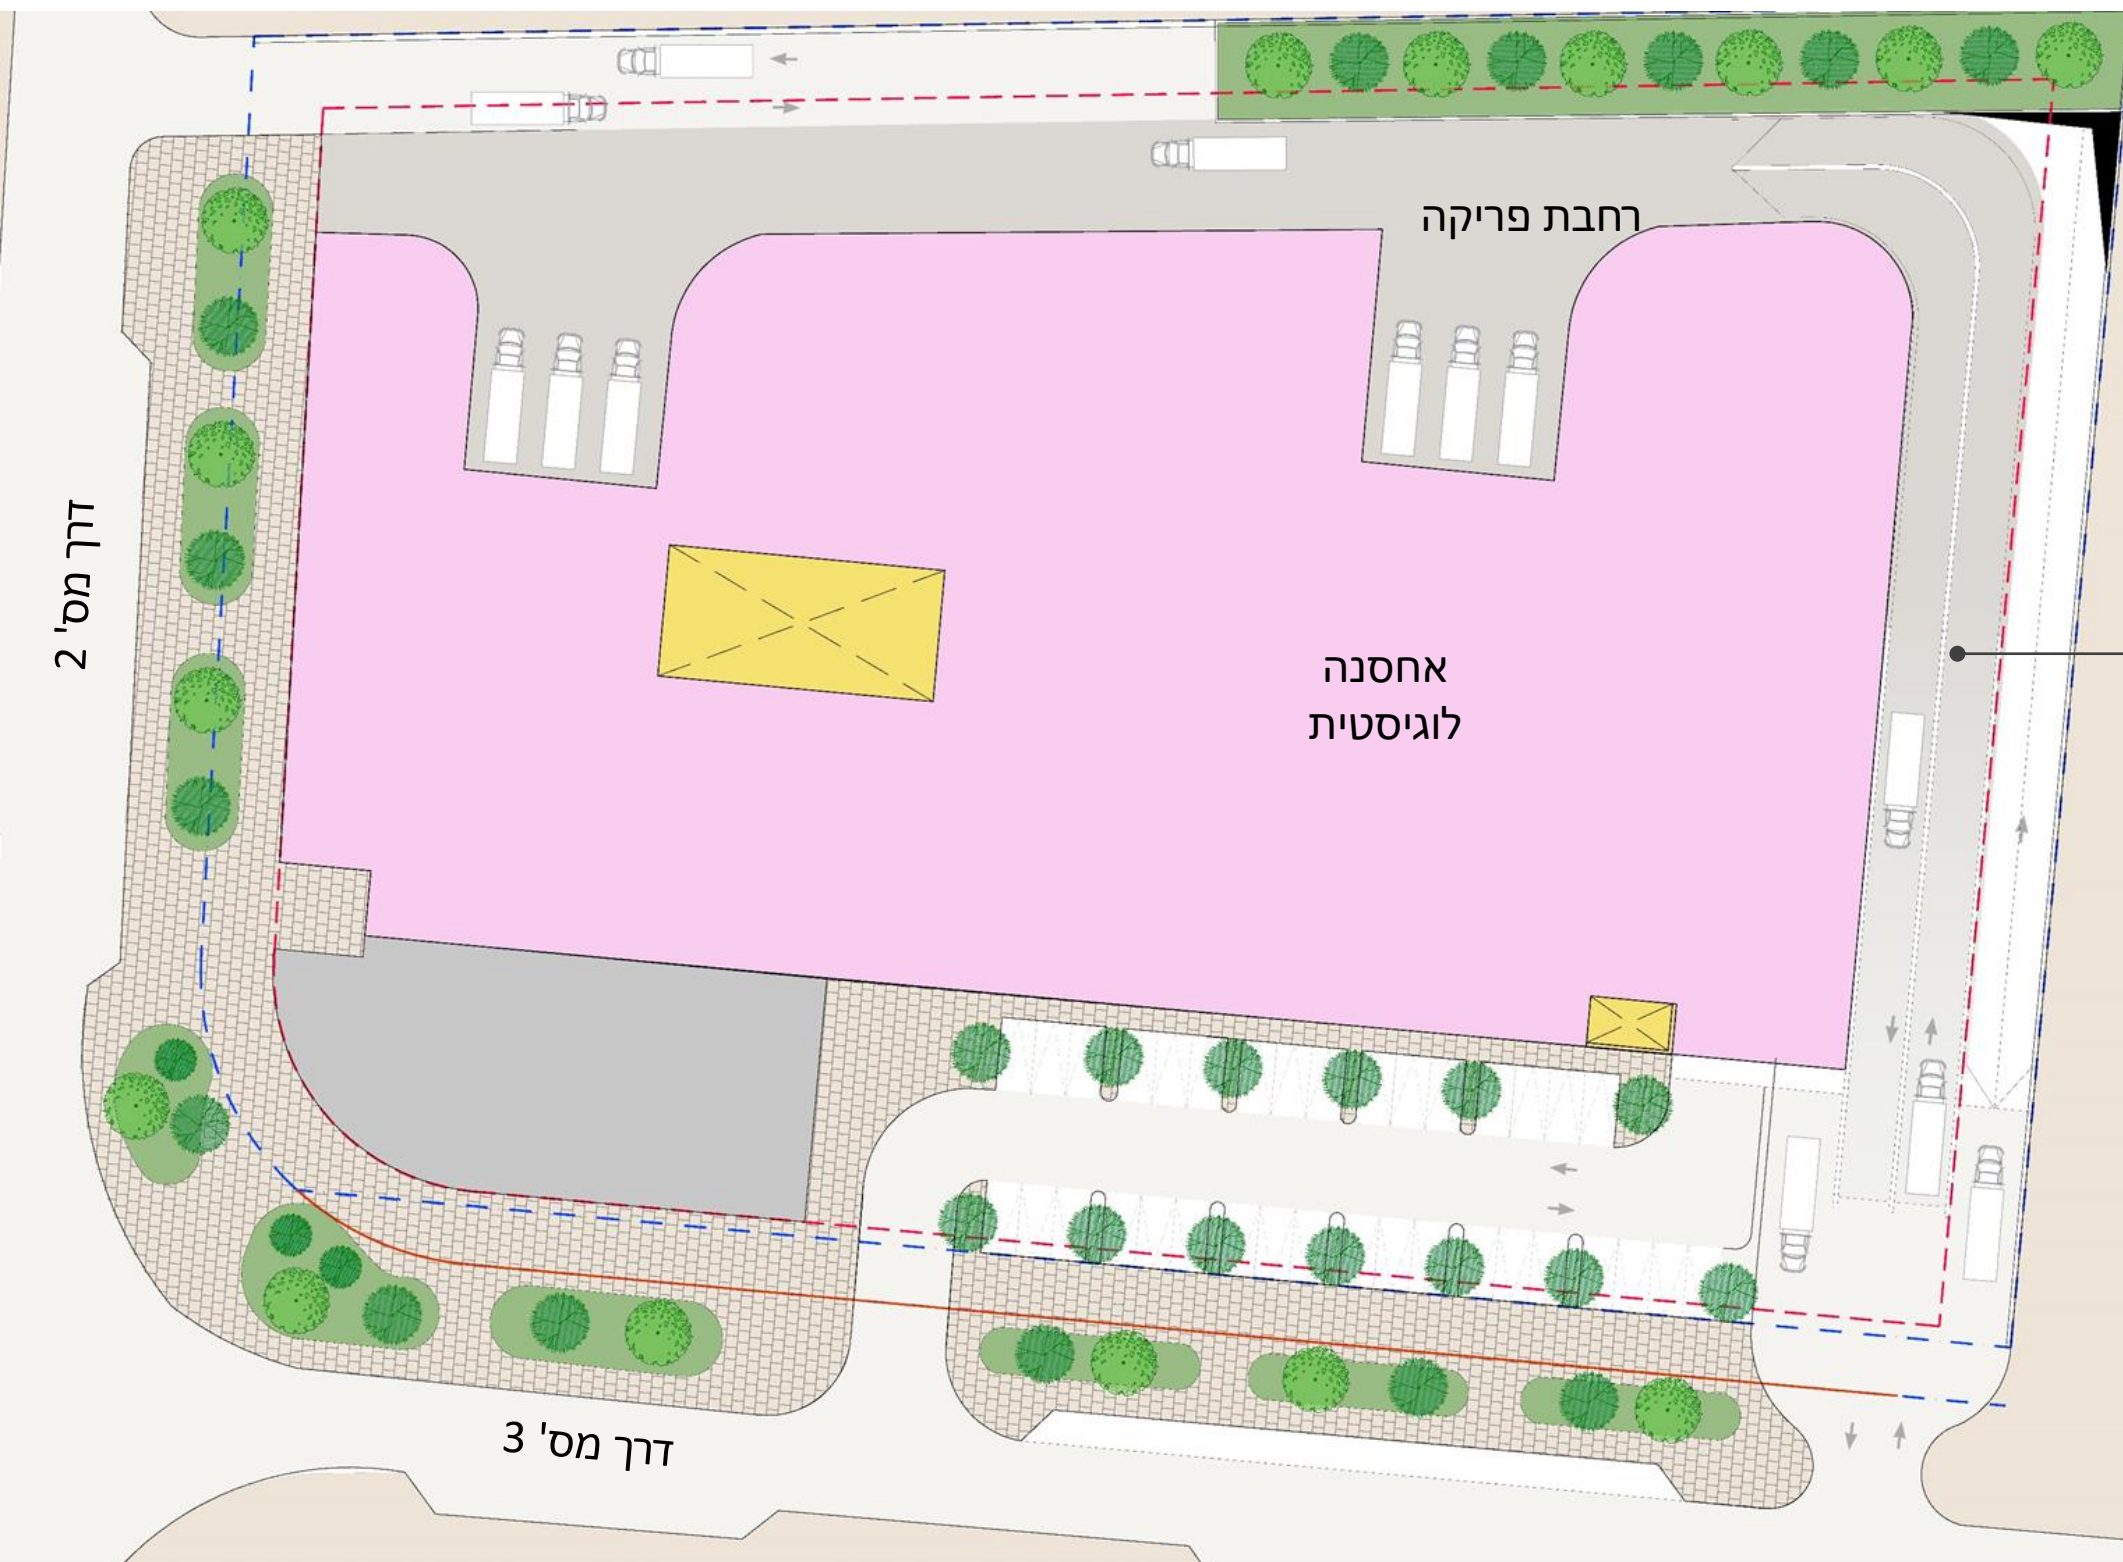


רמפת עליה לקומה 1

אחסנה לוגיסטית

גרעינים, טכני

• שטח קומה ברוטו:
כ- 6300 מ"ר

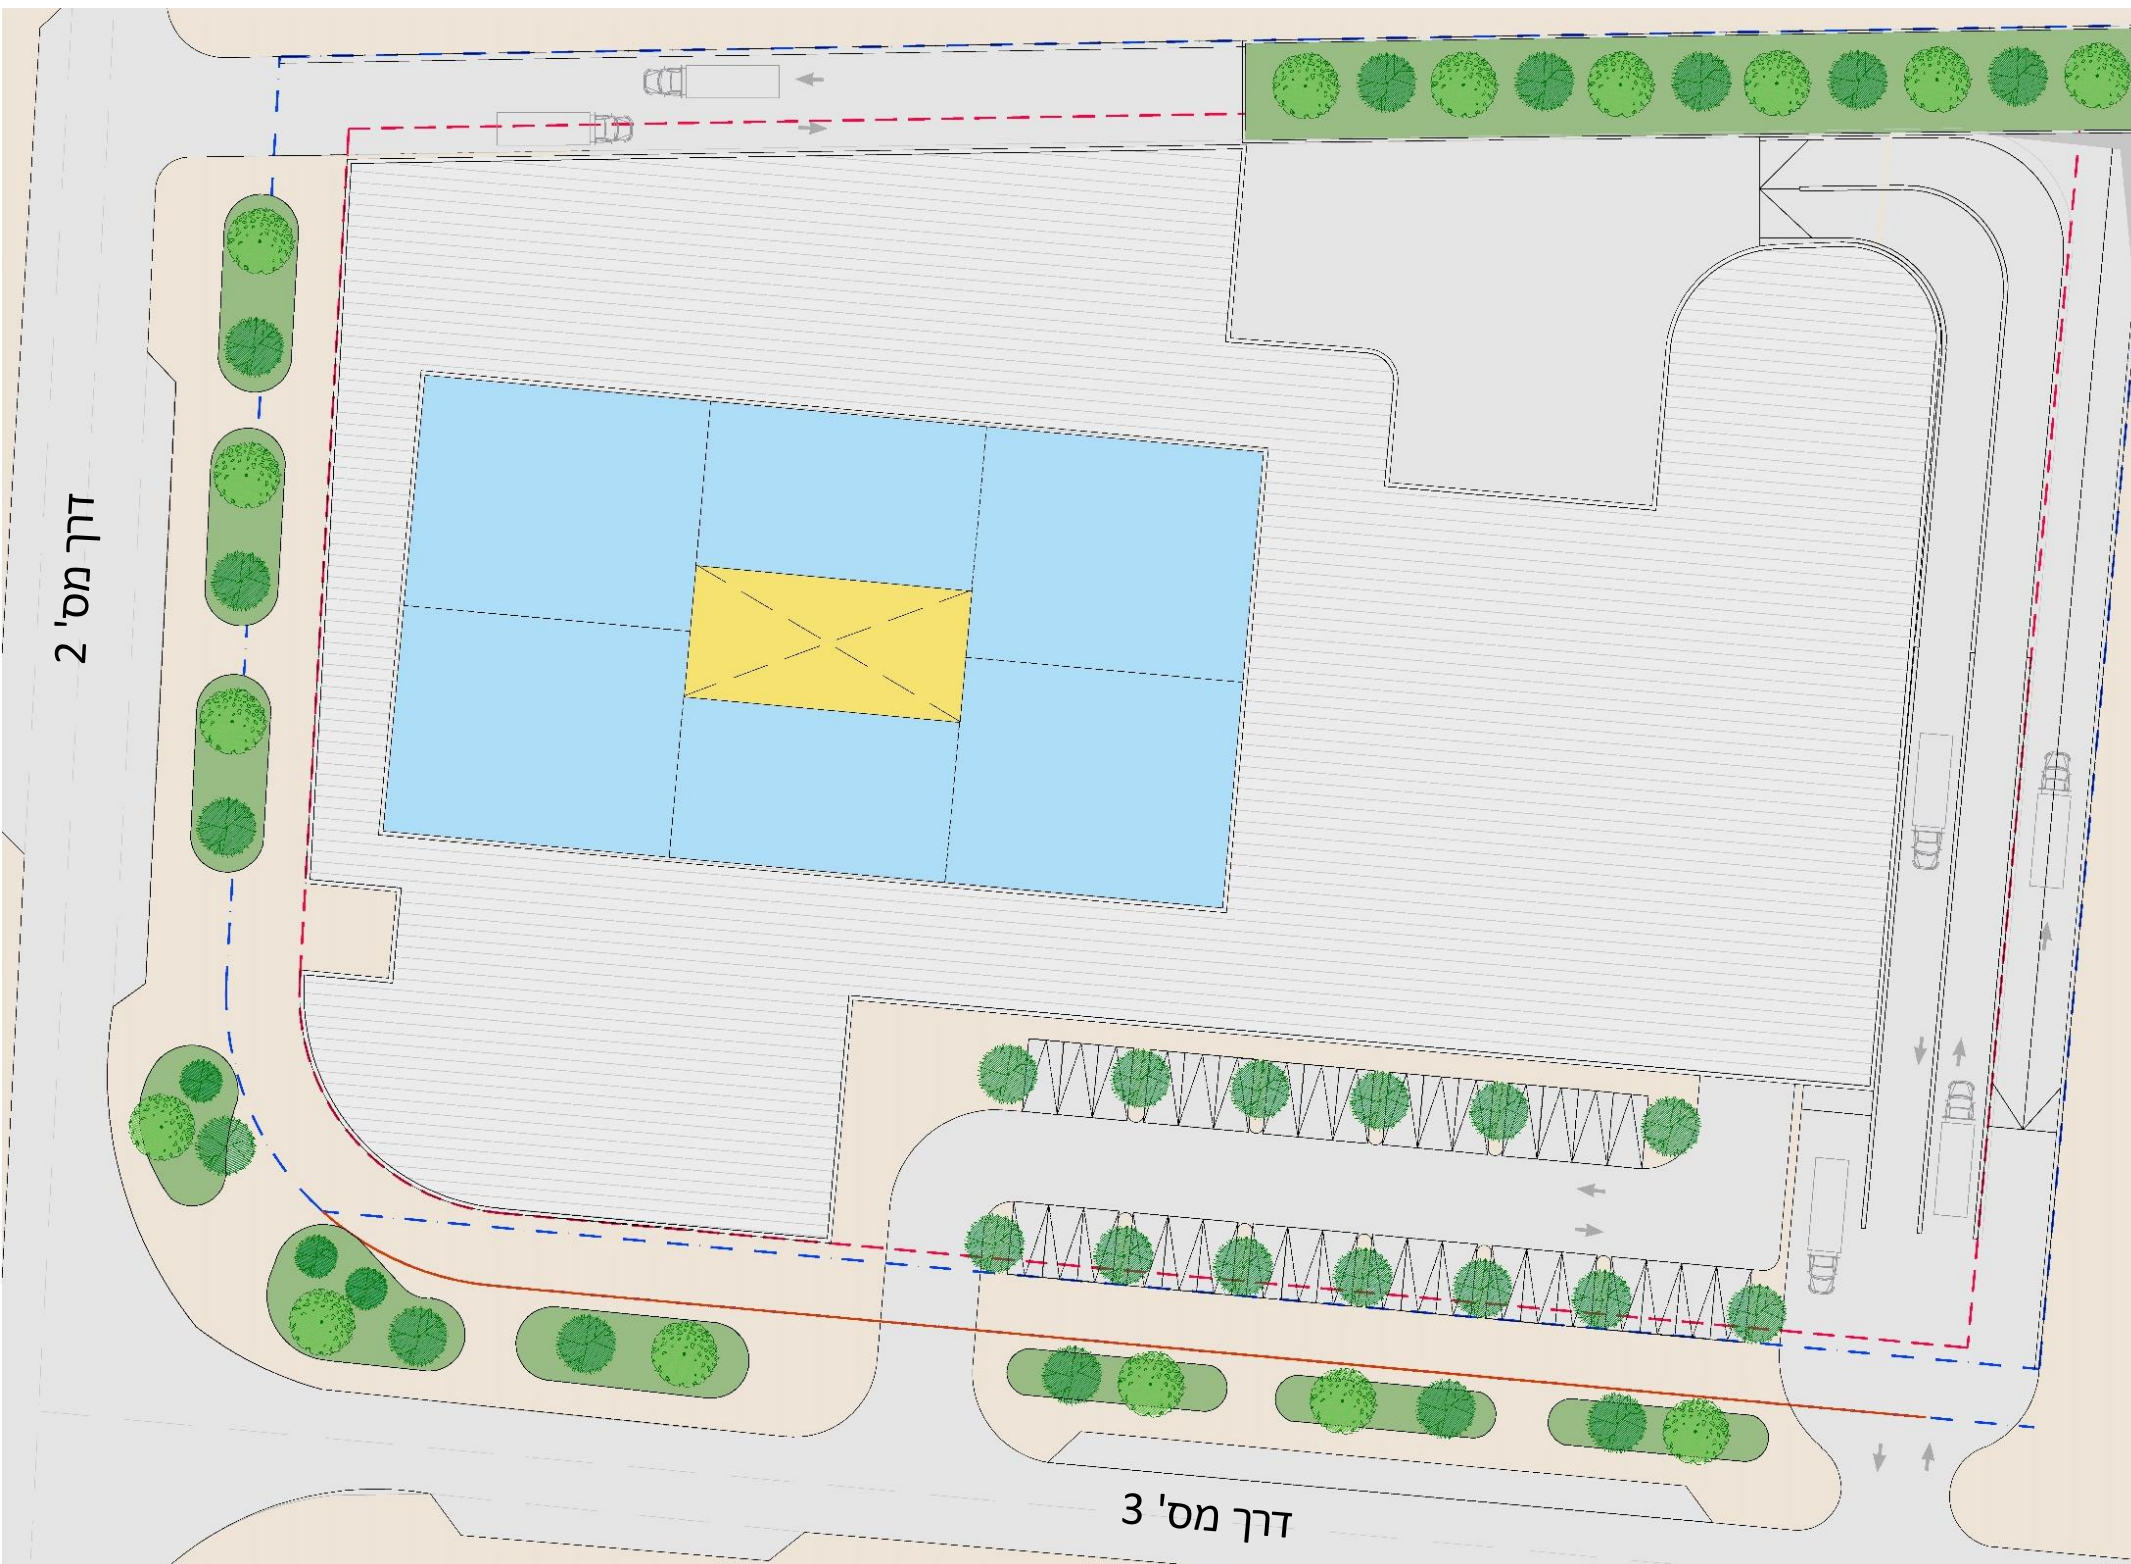


משרדים

גרעינים, טכני

• שטח קומה ברוטו:
כ-1800 מ"ר



תכנון מוצע | תכנית קומת מרתף 1/-2-

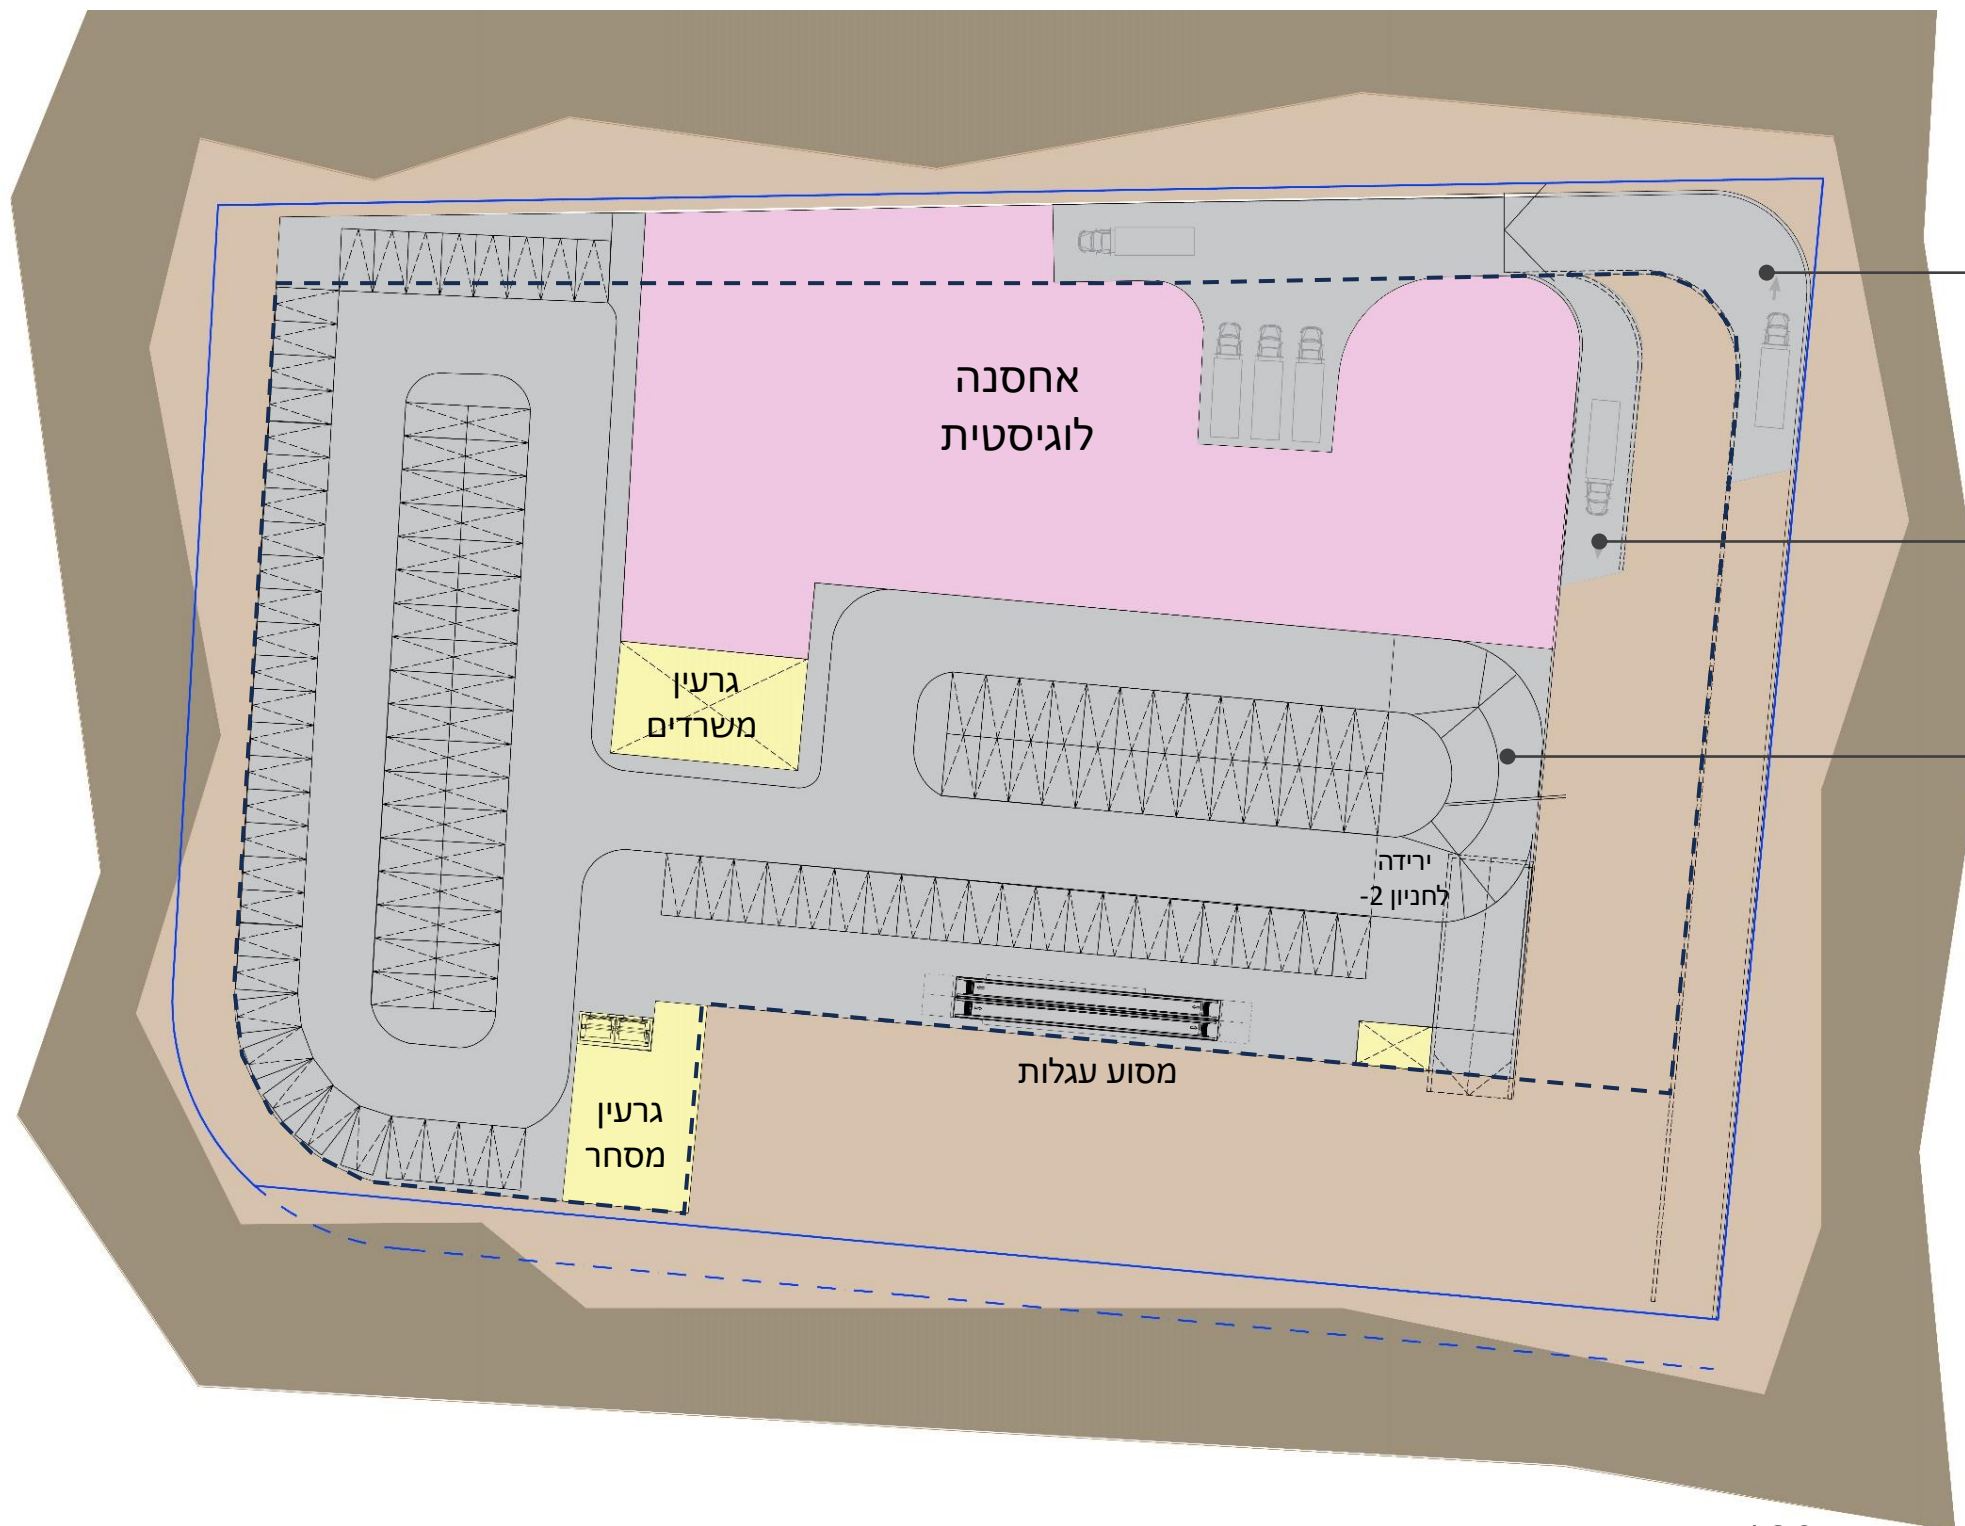

רמפת ירידה למשאיות

רמפת עליה למשאיות

רמפת ירידה
לרכבים פרטיים


אחסנה לוגיסטית

גרעינים, טכני

חניה

• שטח קומה ברוטו:
כ-6670 מ"ר

כ-120 חניות בקומה

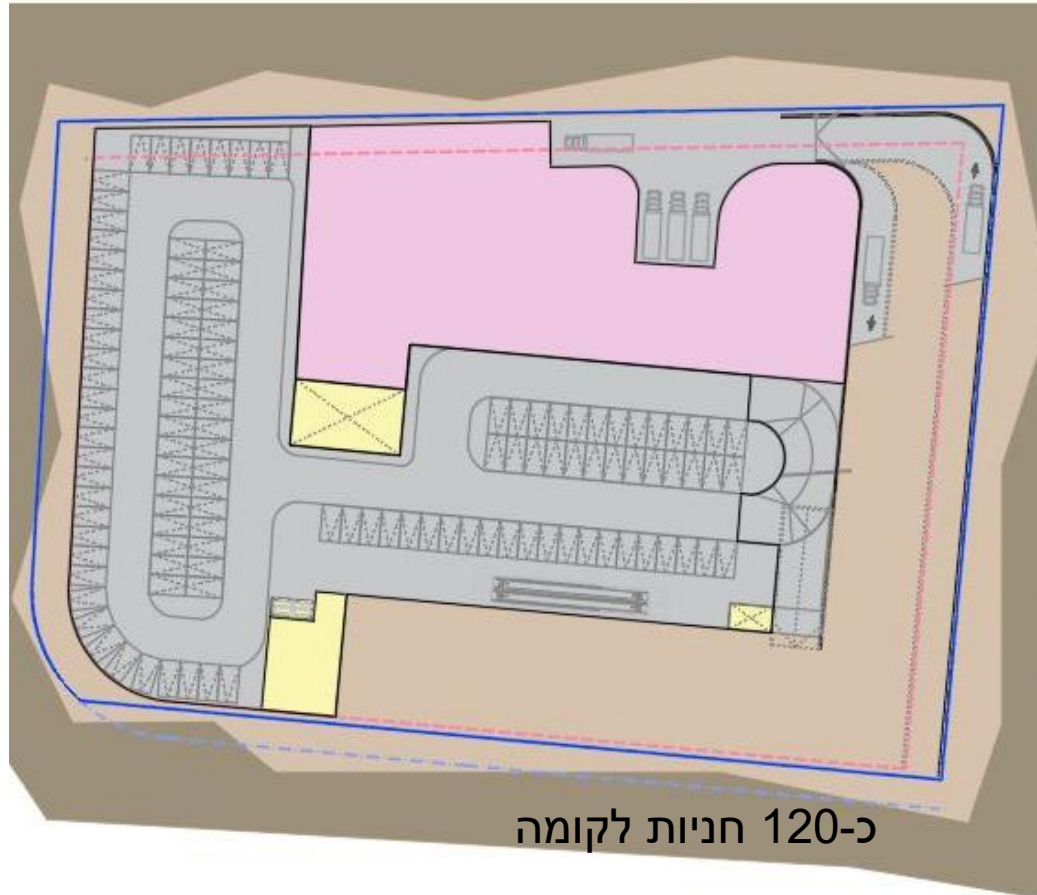

חניות	תקן חניה	שטח	
48	1:35	1660	מסחר
90	1:25	2240	סופר
20	1:300	6100	לוגיסטיקה
54	1:120	6400	משרדים
7	תוספת חניות נכים		
219	סה"כ		

שלב א'
שלב ב'

סה"כ היצע חניה המתוכנן בפרויקט : כ-275 רכבים



תודה רבה!